

Bina Yüksekliği	
2500 mm	
Dış Duvarlar (kalınlık)	
100 mm	
İç Duvarlar (kalınlık)	
60 mm	
Panel Türü	
POLİÜRETTAN Panel	
Çatı Şekli	
Beşik	
Çatı Kaplaması	
TRAPEZ	
Çatı Kaplama Rengi	
KIRMIZI	
Dış Kapı	
Çelik	
İç Kapılar	
Amerikan Panel	
Dış Cephe Boya	
Sandeco	
İç Cephe Boya	
Sandeco	
Tavan Şekli	
Ters tavan	
Saçak Rengi	
Antrasit	
Saçak Çıkması	
30 cm	
Yağmur Oluğu	
Metal	
Yağmur Oluğu Rengi	
Antrasit	
Yağmur İniş Borusu	
Metal	
Yağmur İniş Borusu Rengi	
Antrasit	
Açıklama	

iç cephede alçıpan kaplama yapılacaktır.

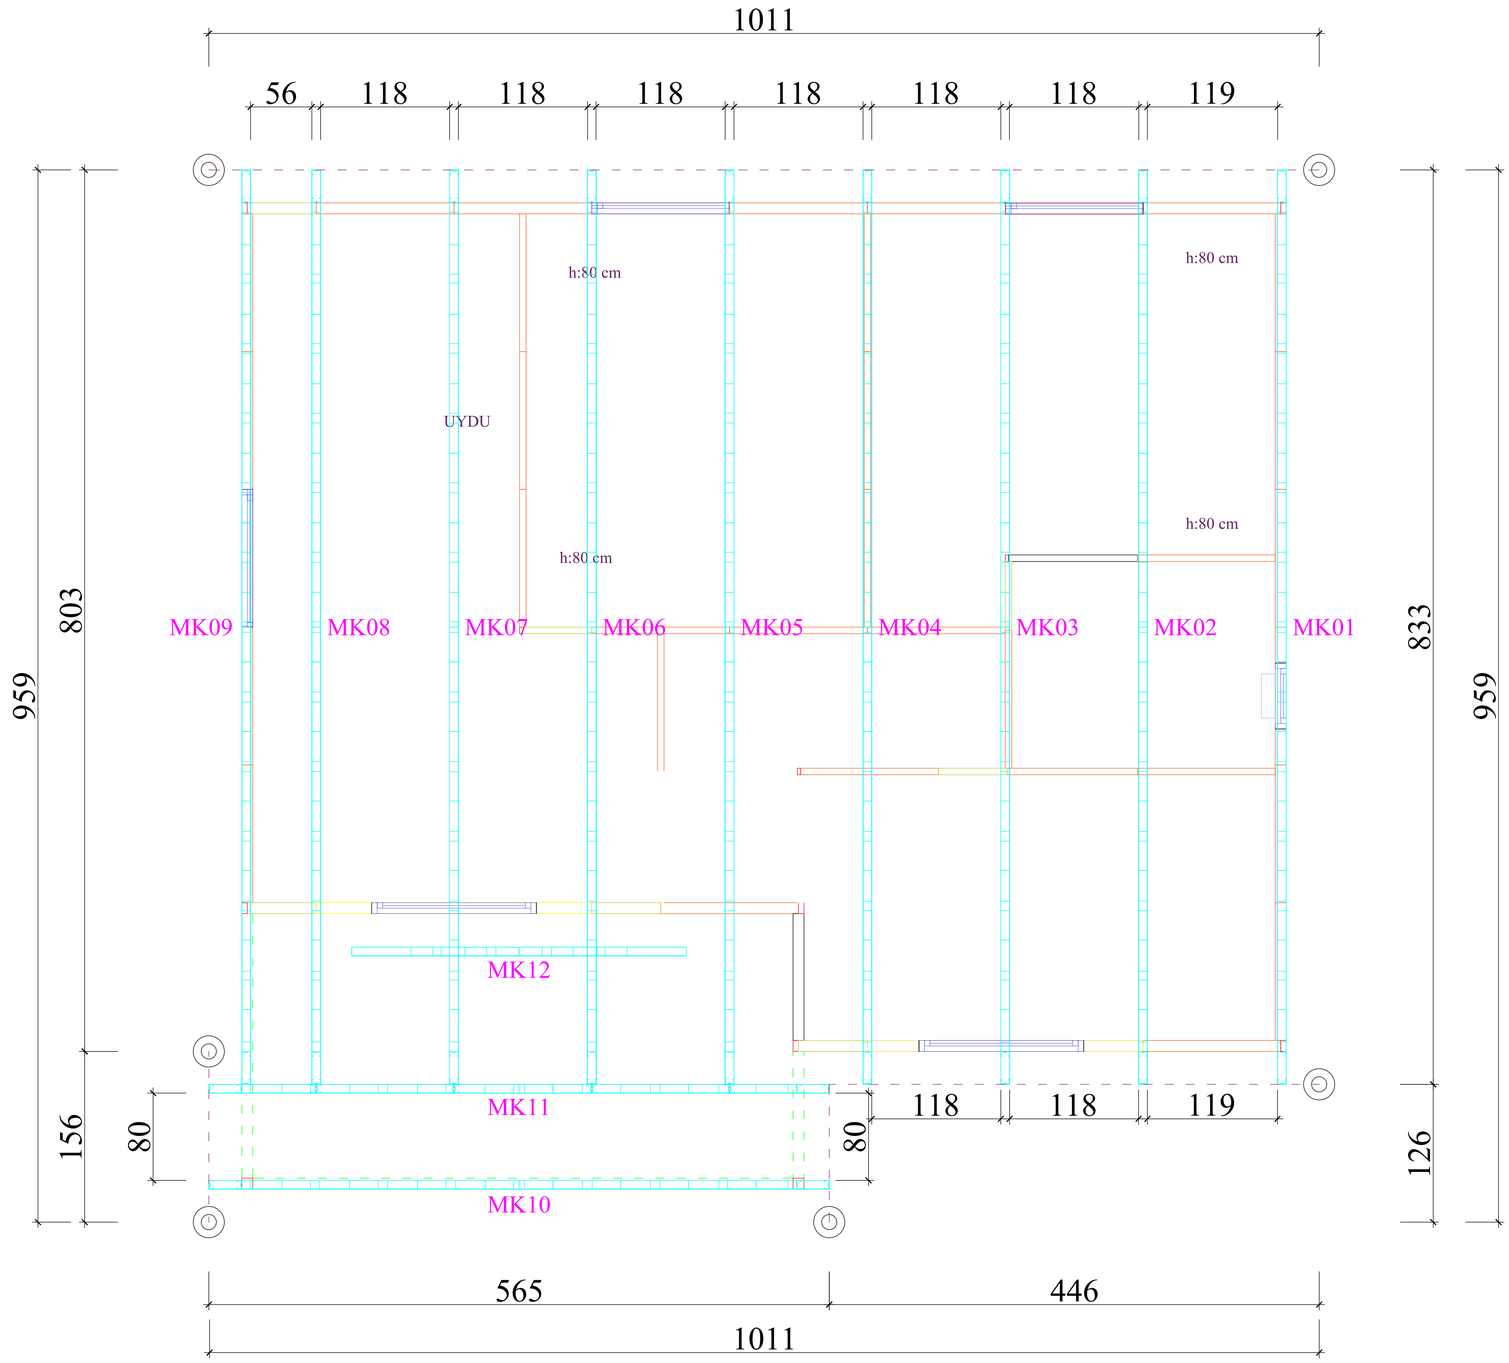

MAKAS VE DERE YERLEŞİM PLANI

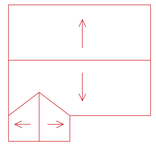


ÇATI ŞEKLİ


1-) Aşıklar 60 cm aralıklarla monte edilecektir

2-) Mahya aşığı 20 cm de monte edilecektir

MONTAJ DETAYLARI

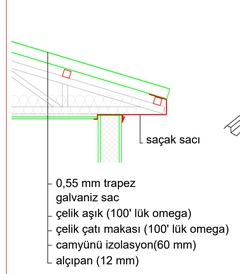

Çatı Detayı

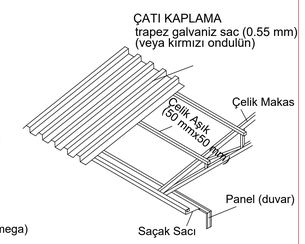

Çatı Detayı

ÇATI DETAYLARI

		DOĞAN PREFABRİK	
Satış Temsilcisi	LOKMAN SAYIM	ÇİZEN	BATUHAN TINMAZ