
Bina Yüksekliği	
2500 mm	
Dış Duvarlar (kalınlık)	
100 mm	
İç Duvarlar (kalınlık)	
60 mm	
Panel Türü	
POLİÜRETTAN Panel	
Çatı Şekli	
Beşik	
Çatı Kaplaması	
TRAPEZ	
Çatı Kaplama Rengi	
KIRMIZI	
Dış Kapı	
Çelik	
İç Kapılar	
Amerikan Panel	
Dış Cephe Boya	
Sandeco	
İç Cephe Boya	
Sandeco	
Tavan Şekli	
Ters tavan	
Saçak Rengi	
Antrasit	
Saçak Çıkması	
30 cm	
Yağmur Oluğu	
Metal	
Yağmur Oluğu Rengi	
Antrasit	
Yağmur İniş Borusu	
Metal	
Yağmur İniş Borusu Rengi	
Antrasit	
Açıklama	


iç cephede alçıpan kaplama yapılacaktır.

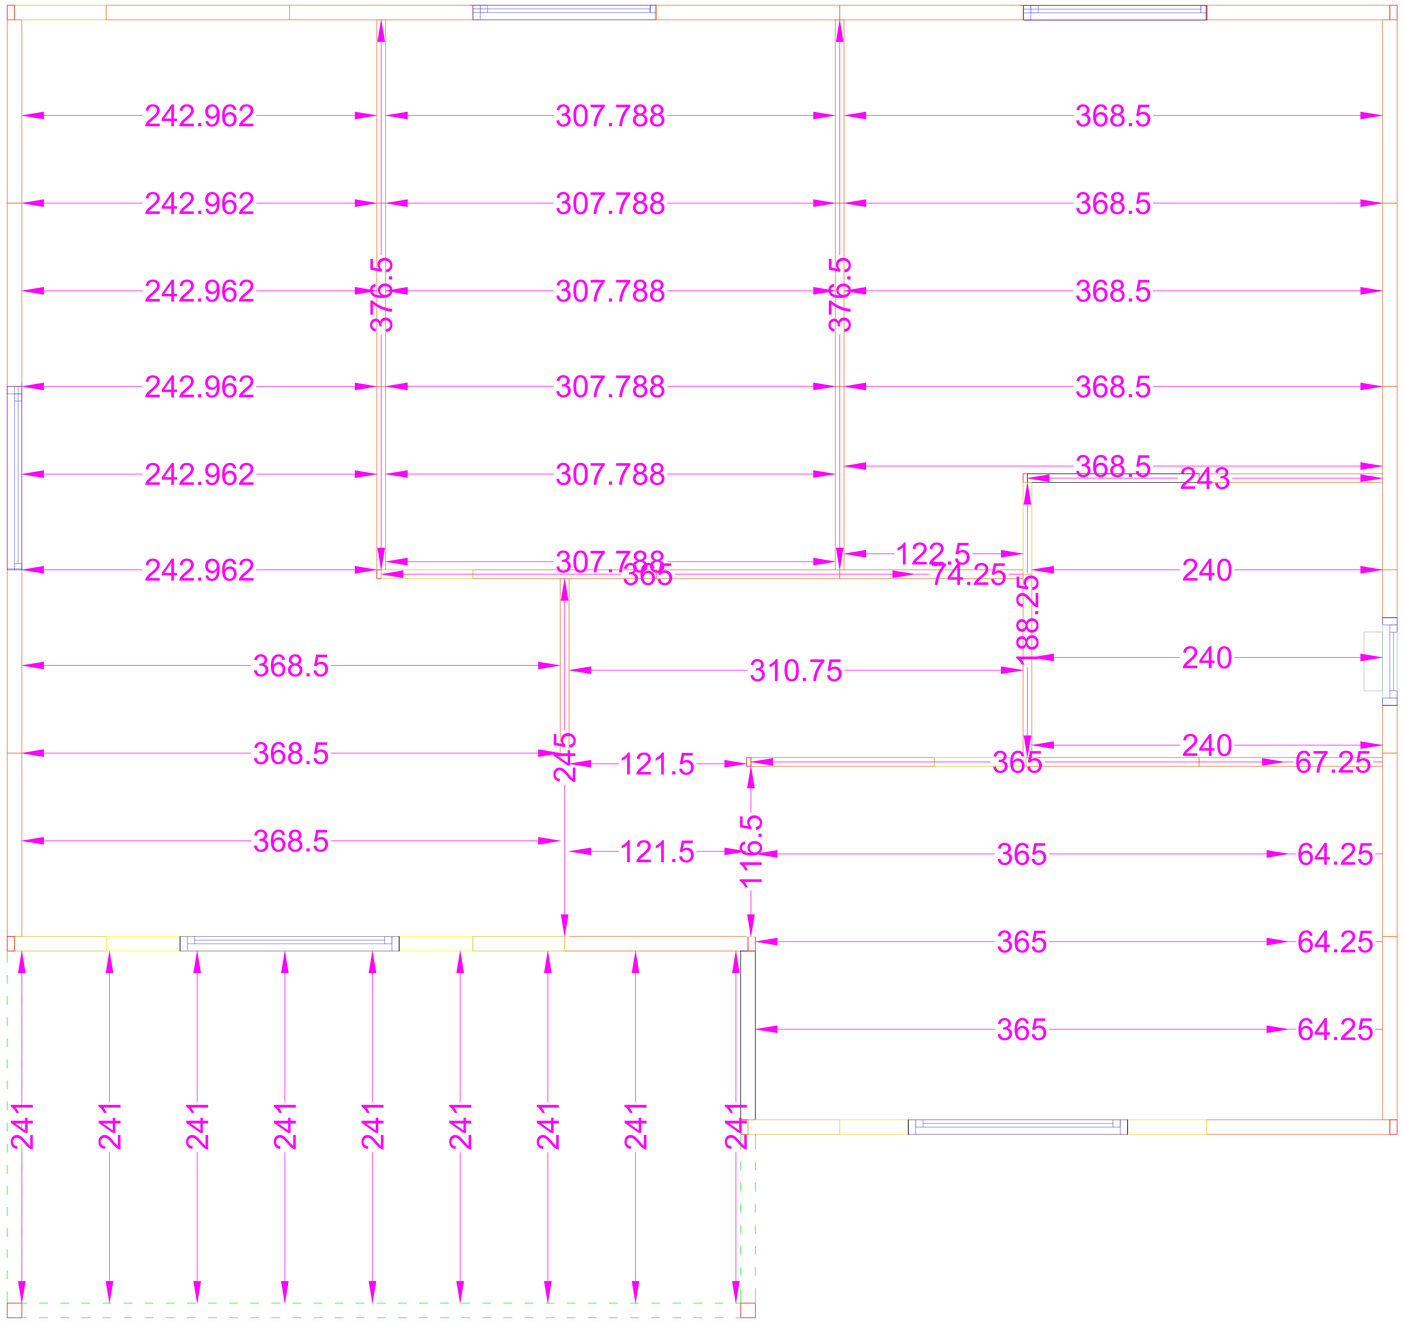

TAVAN OMEGA YERLEŞİM PLANI

1-)ters tavan yapılacak
(Omega profiller 60 cm de bir monte edilecek)

MONTAJ DETAYLARI

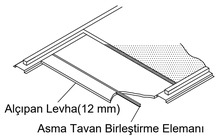

MONTAJ DETAYLARI

			DOĞAN PREFABRİK
Satış Temsilcisi	LOKMAN SAYIM	ÇİZEN	BATUHAN TINMAZ

LOFTEV