1 · ZEMİN KAT — kıyas kopyası (duvar yüzünden yüzüne ölçüler) · İE-22 CK-01 · 28.10.2026 · ölçüler cm · TASLAK

ZEMİN KAT · KIYAS KOPYASI (Lokman 14:00): aks/pano ölçüleri yok, duvar yüzünden yüzüne zincirler; asıl planla karşılaştırma için

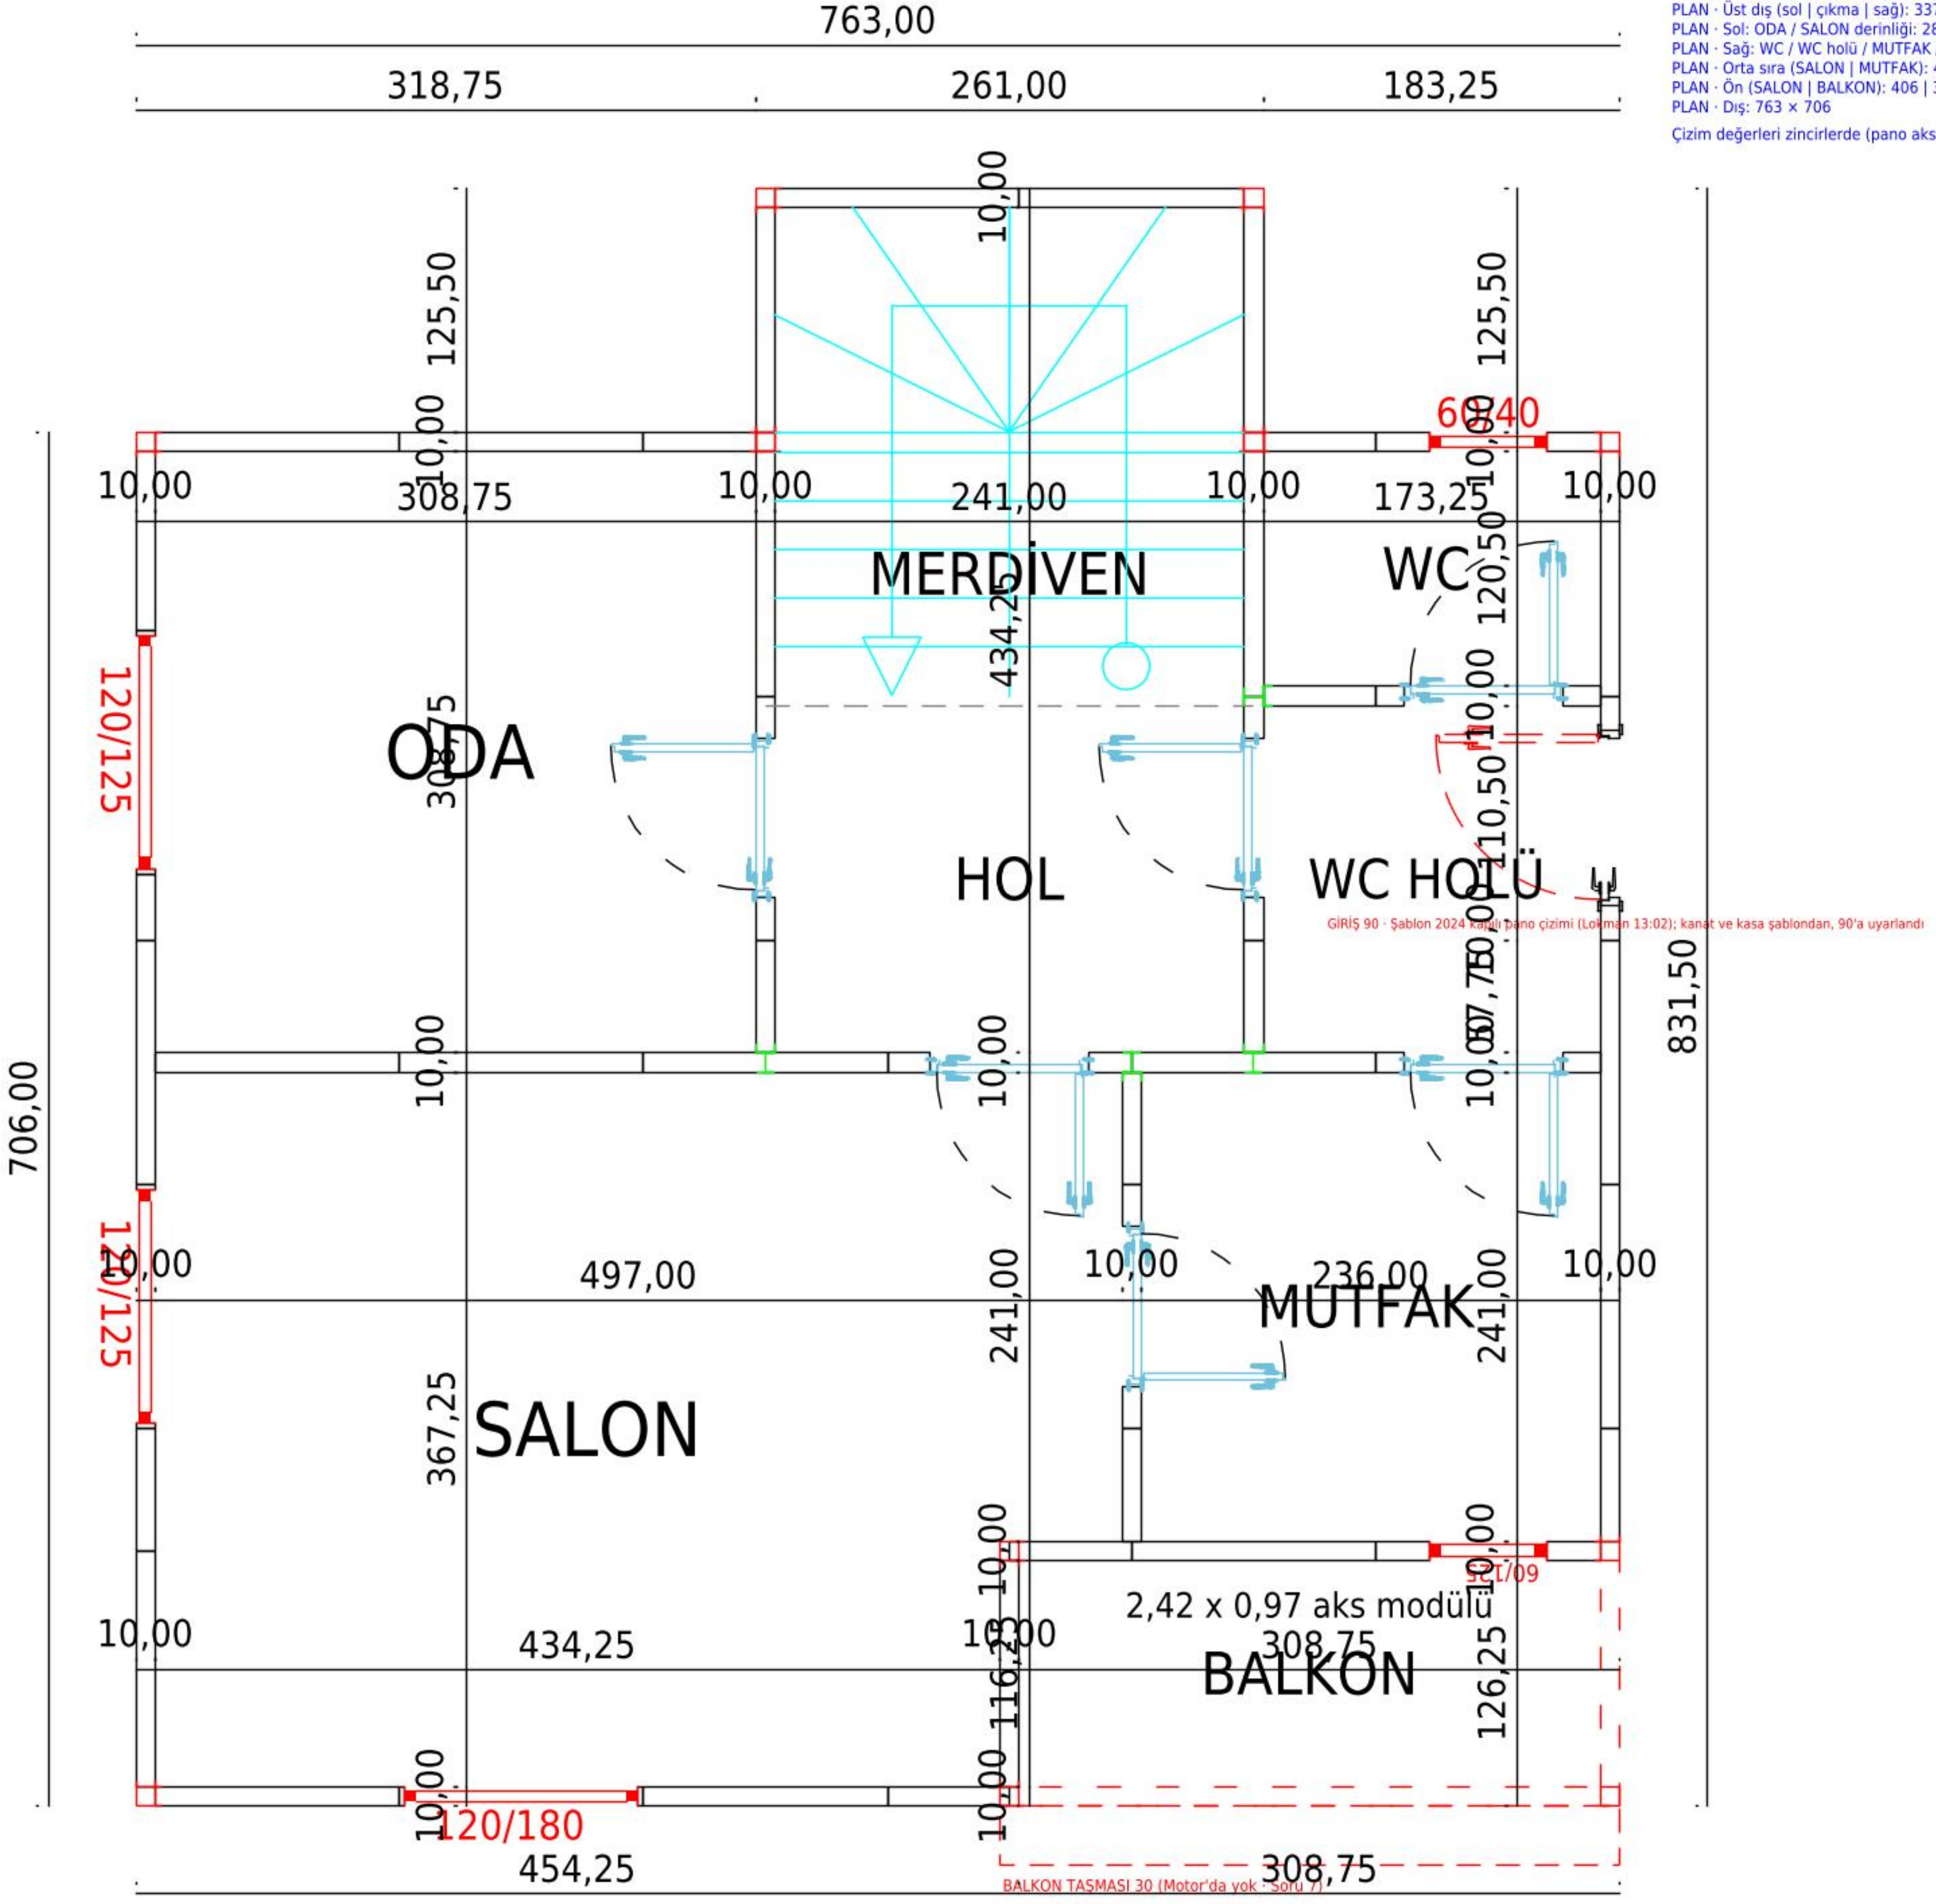
763,00
318,75
261,00
183,25
125,50
10,00
125,50
60/40
10,00
308,75
10,00
241,00
10,00
173,25
10,00
MERDİVEN
434,25
WC
120,50
120/125
ODA
308,75
HOL
WC HOLÜ
110,50
831,50
706,00
107,75
10,00
10,00
10,00
120/125
10,00
497,00
10,00
236,00
10,00
241,00
241,00
MUTFAK
SALON
367,25
60/125
2,42 x 0,97 aks modülü
10,00
434,25
10,00
308,75
116,25
BALKON
126,25
10,00
120/180
454,25
308,75

GİRİŞ 90 · Şablon 2024 kapılı pano çizimi (Lokman 13:02); kanat ve kasa şablondan, 90'a uyarlandı

BALKON TAŞMASI 30 (Motor'da yok · Soru 7)

PLAN · Arka sıra (ODA | kova | WC): 327 | 200 | 196
PLAN · Üst dış (sol | çıkma | sağ): 337 | 220 | 206
PLAN · Sol: ODA / SALON derinliği: 287 / 389
PLAN · Sağ: WC / WC holü / MUTFAK / BALKON: 125 / 152
PLAN · Orta sıra (SALON | MUTFAK): 457 | 276
PLAN · Ön (SALON | BALKON): 406 | 337
PLAN · Dış: 763 × 706

Çizim değerleri zincirlerde (pano aksından: 125,5 ızgaras

2 · 1. KAT — kıyas kopyası · İE-22 CK-01 · 28.10.2026 · ölçüler cm · TASLAK

1. KAT · KIYAS KOPYASI (Lokman 14:00): aks/pano ölçüleri yok, duvar yüzünden yüzüne zincirler; asıl planla karşılaştırma için

PLAN · Arka sıra (ODA 1 | kova | BANYO): 327 | 200 | 196
PLAN · Üst dış (sol | çıkma | sağ): 337 | 220 | 206
PLAN · Dış: 763 × 706

Çizim değerleri zincirlerde (pano aksından: 125,5 ızgaras

165

lük duvarlar). Fark = ızgaraya oturtma.

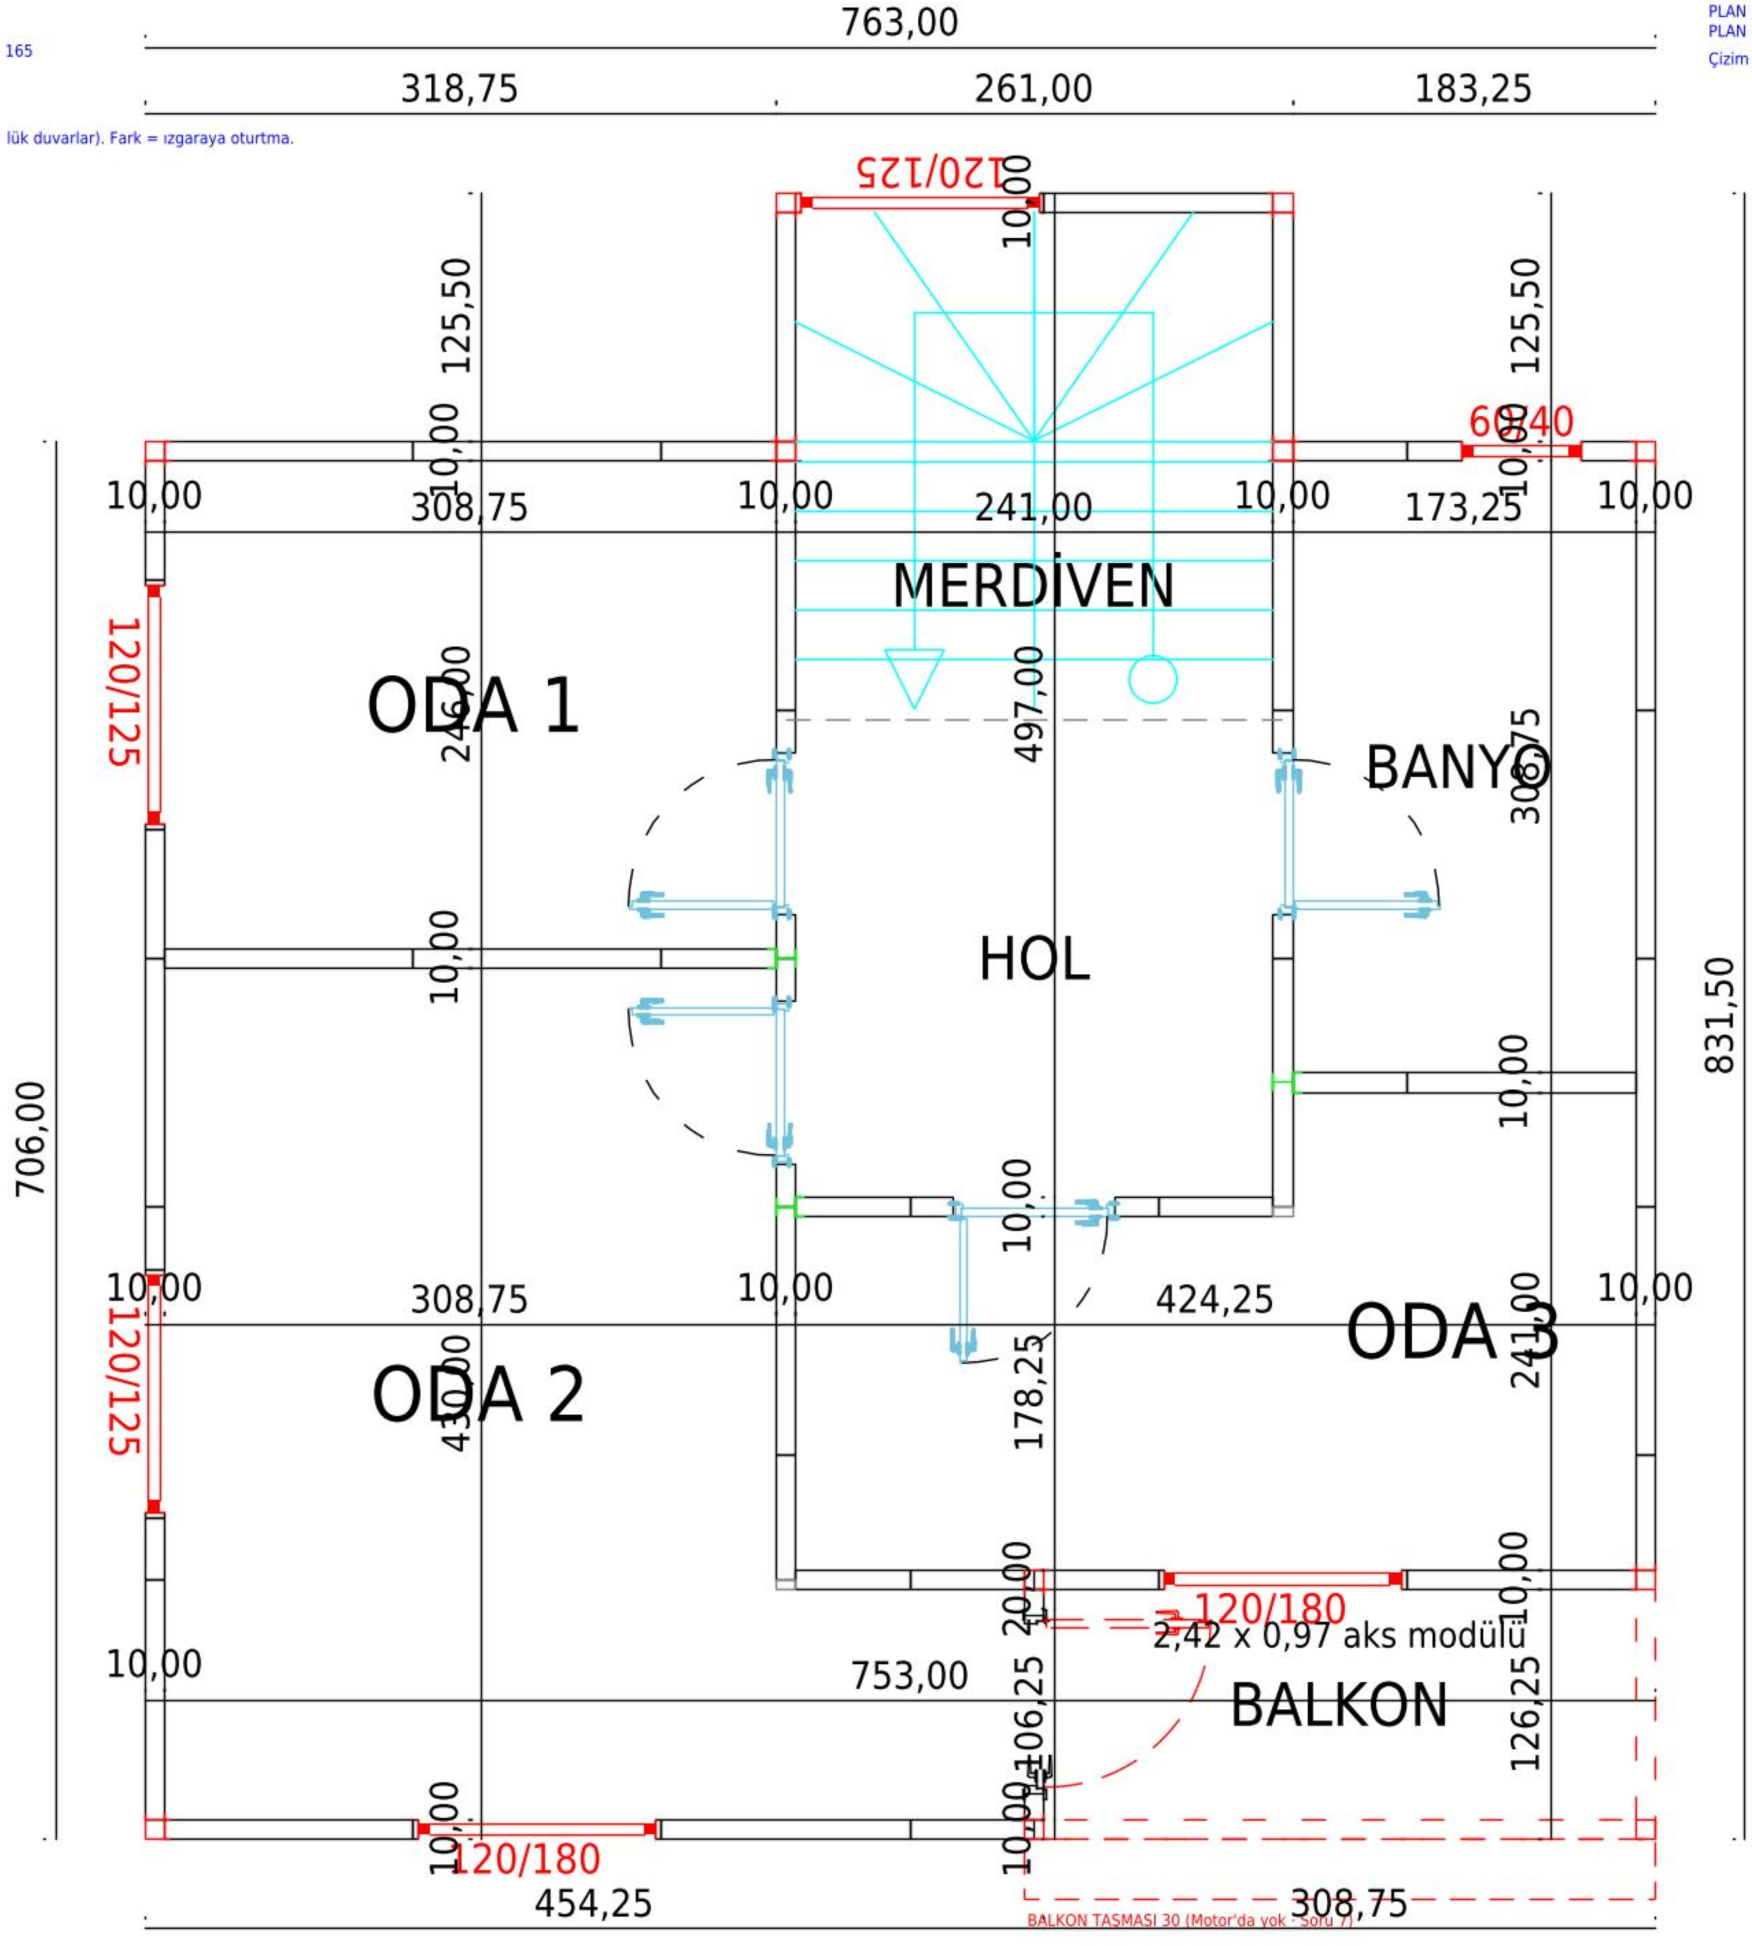
763,00
318,75
261,00
183,25
120/125
10,00
125,50
125,50
60/40
10,00
10,00
308,75
10,00
241,00
10,00
173,25
10,00
MERDİVEN
120/125
ODA 1
246,00
497,00
BANYO
308,75
HOL
10,00
831,50
706,00
10,00
10,00
10,00
10,00
308,75
10,00
424,25
ODA 3
10,00
120/125
ODA 2
430,00
178,25
241,00
20,00
120/180
2,42 x 0,97 aks modülü
10,00
10,00
753,00
BALKON
106,25
126,25
10,00
10,00
120/180
454,25
308,75
BALKON TAŞMASI 30 (Motor'da yok · Soru 7)

ZEMİN KAT · 763 × 706 · Şablon 2024 blok adlarıyla · İE-22 (28.10.2026)

KAT PLANI — AKSLI

zemin kat | 5 PANO + 115,5 cm x 5 PANO + 58,5 cm | 763 × 706 (10 + 5 × 125,5 + 115,5 + 10) cm | Model ve ölçüler: cm | 125,5 cm aks dü

MERDİVEN KOVASI 2 pano (akslar 323,75 / 574,75; iç 241) + çıkma 1 pano · çift kollu U, kol 120.50, 5 + 6 dönel + 5 = 16 rıht (282/16 = 17,6), basamak 25 — düzen Lokman'ın planından (13:00), ölçü
Çıkma duvarları akslara ortalı 10'luk dış pano; arka duvar ek yerlerinde (261→318,75 ve 579,75→637,5 kesik panolar) H simgesi yok · zeminde kovaya giriş: önü açık (Motor `acik_sinirlar`; planda ön d

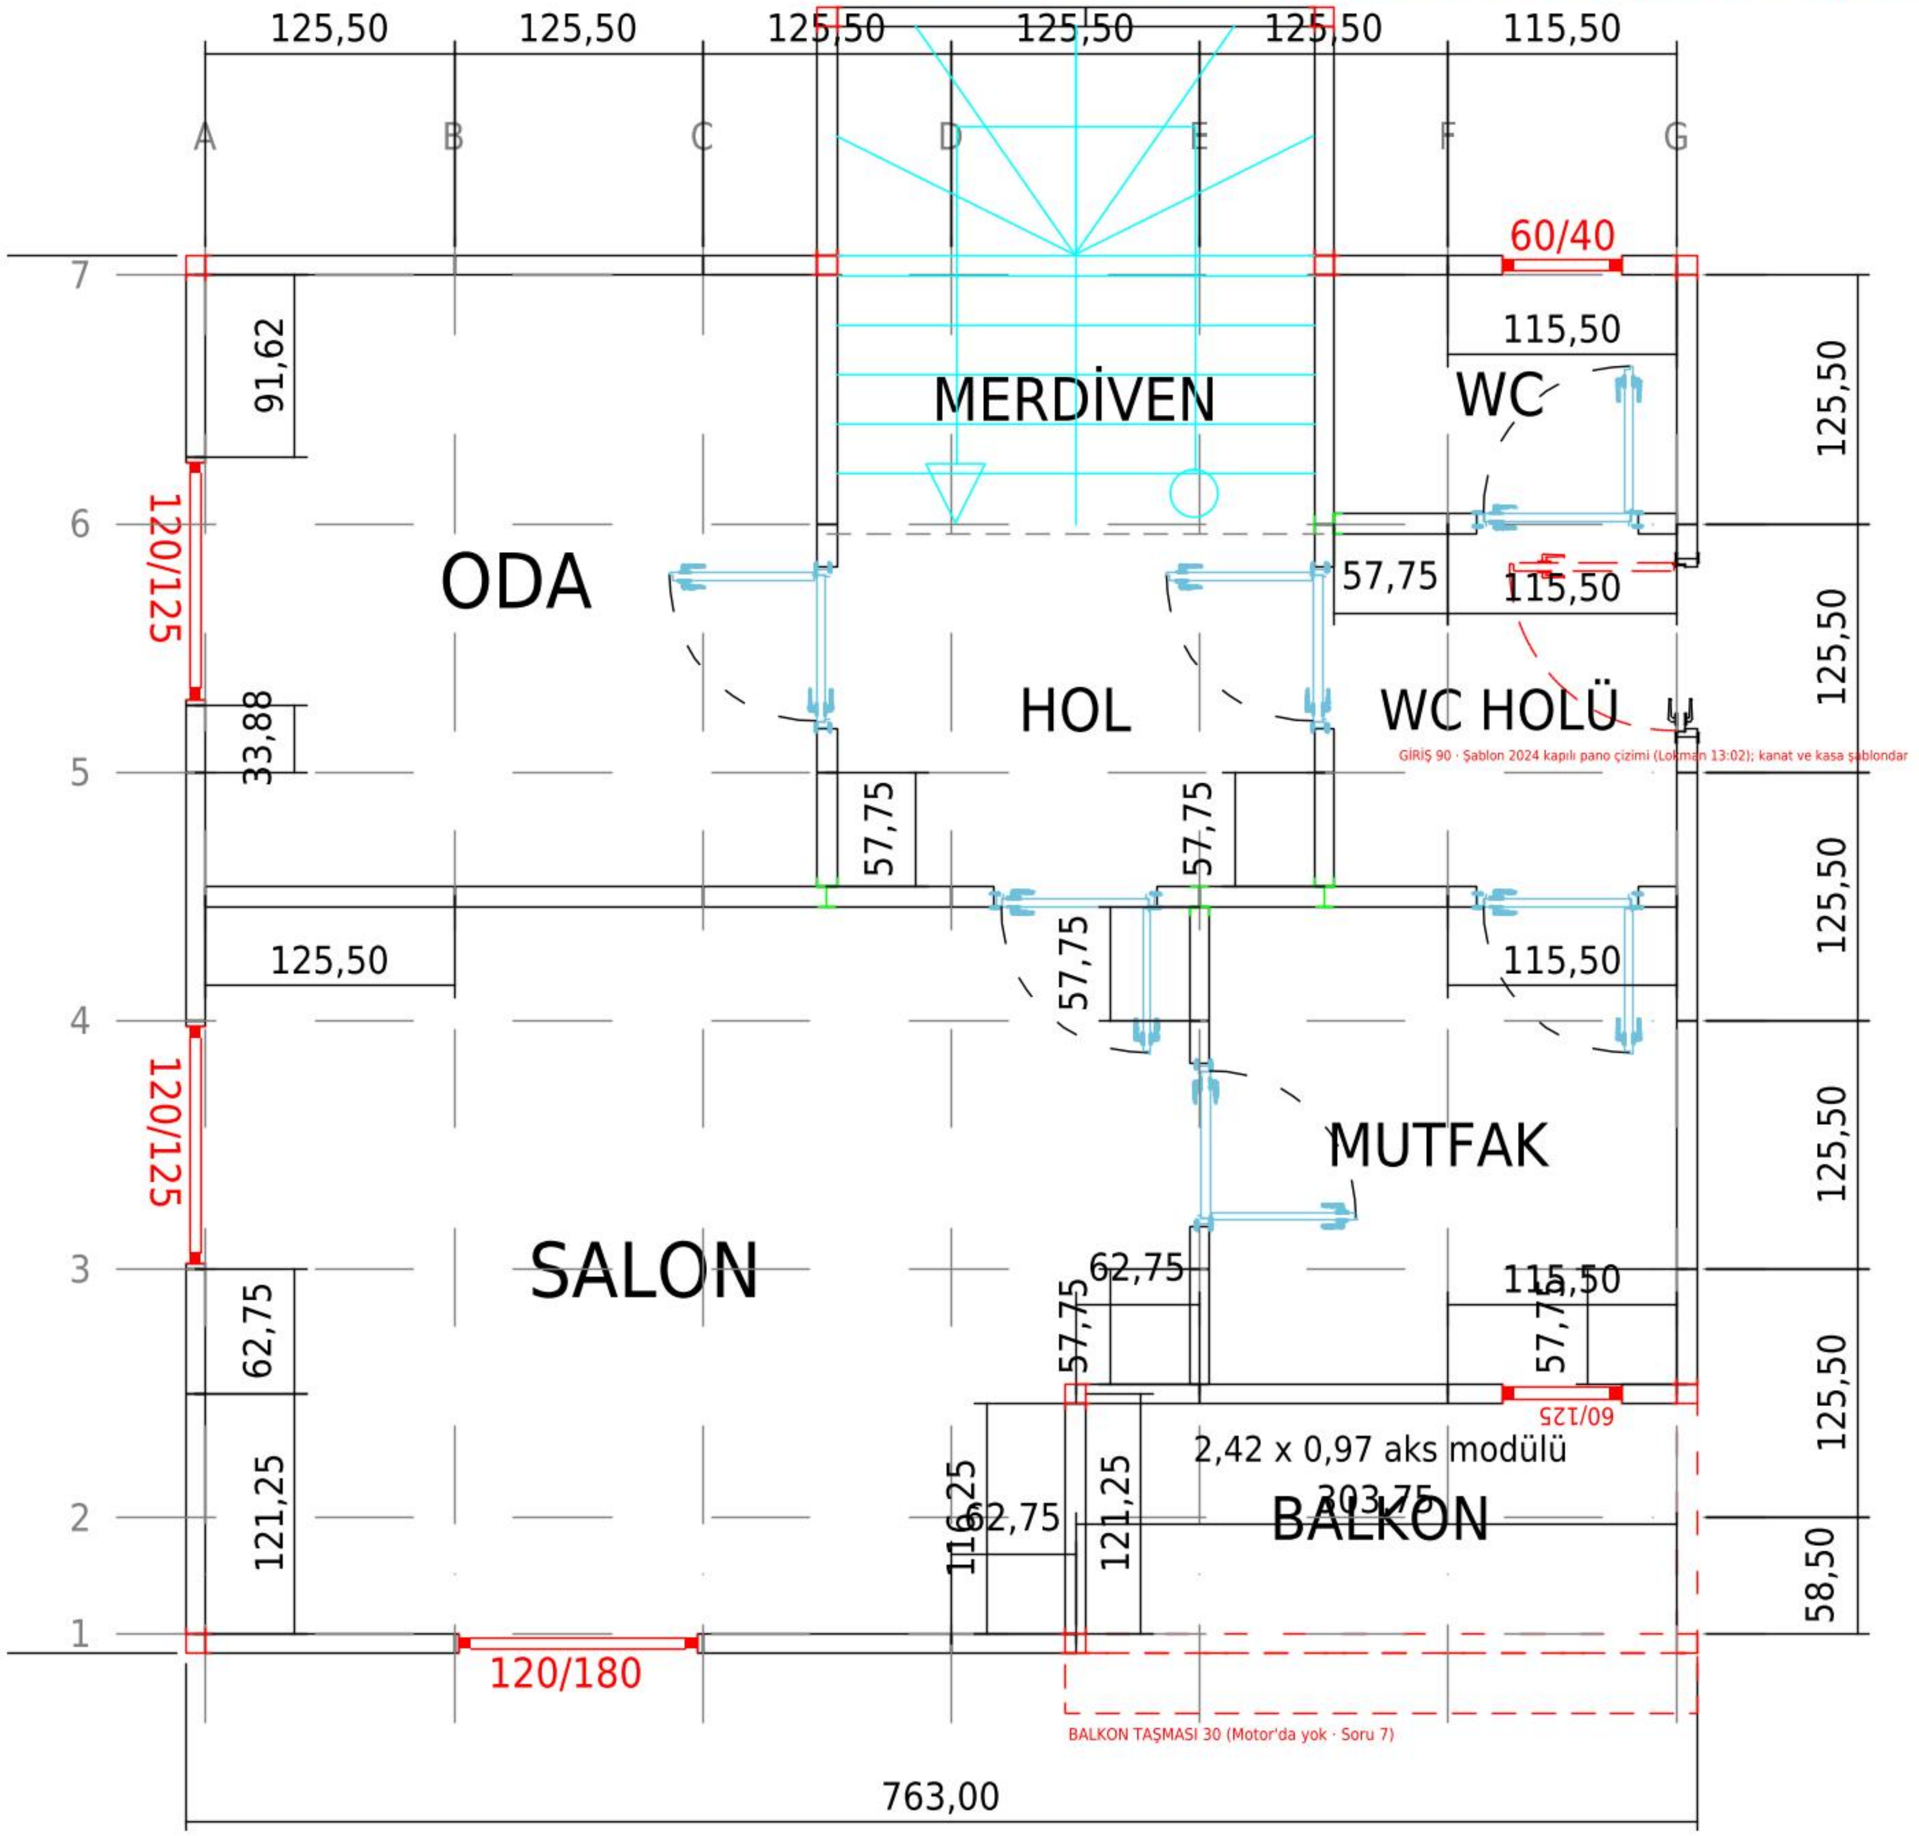
125,50
125,50
125,50
125,50
125,50
115,50
A
B
C
D
E
F
G
7
6
5
4
3
2
1
60/40
115,50
125,50
91,62
MERDİVEN
WC
120/125
ODA
57,75
115,50
125,50
HOL
WC HOLÜ
33,88
57,75
57,75
125,50
125,50
57,75
115,50
120/125
MUTFAK
125,50
SALON
62,75
62,75
115,50
57,75
57,75
60/125
2,42 x 0,97 aks modülü
125,50
121,25
116,25
62,75
121,25
303,75
BALKON
58,50
120/180
763,00

GİRİŞ 90 · Şablon 2024 kapılı pano çizimi (Lokman 13:02); kanat ve kasa şablondar

BALKON TAŞMASI 30 (Motor'da yok · Soru 7)

1. KAT · 763 × 706 · Şablon 2024 blok adlarıyla · İE-22 (28.10.2026)

KAT PLANI — AKSLI

CK-01 birinci kat | 5 PANO + 115,5 cm x 5 PANO + 58,5 cm | 763 × 706 (10 + 5 × 125,5 + 115,5 + 10) cm | Model ve ölçüler: cm | 125,5 cm aks düzeni

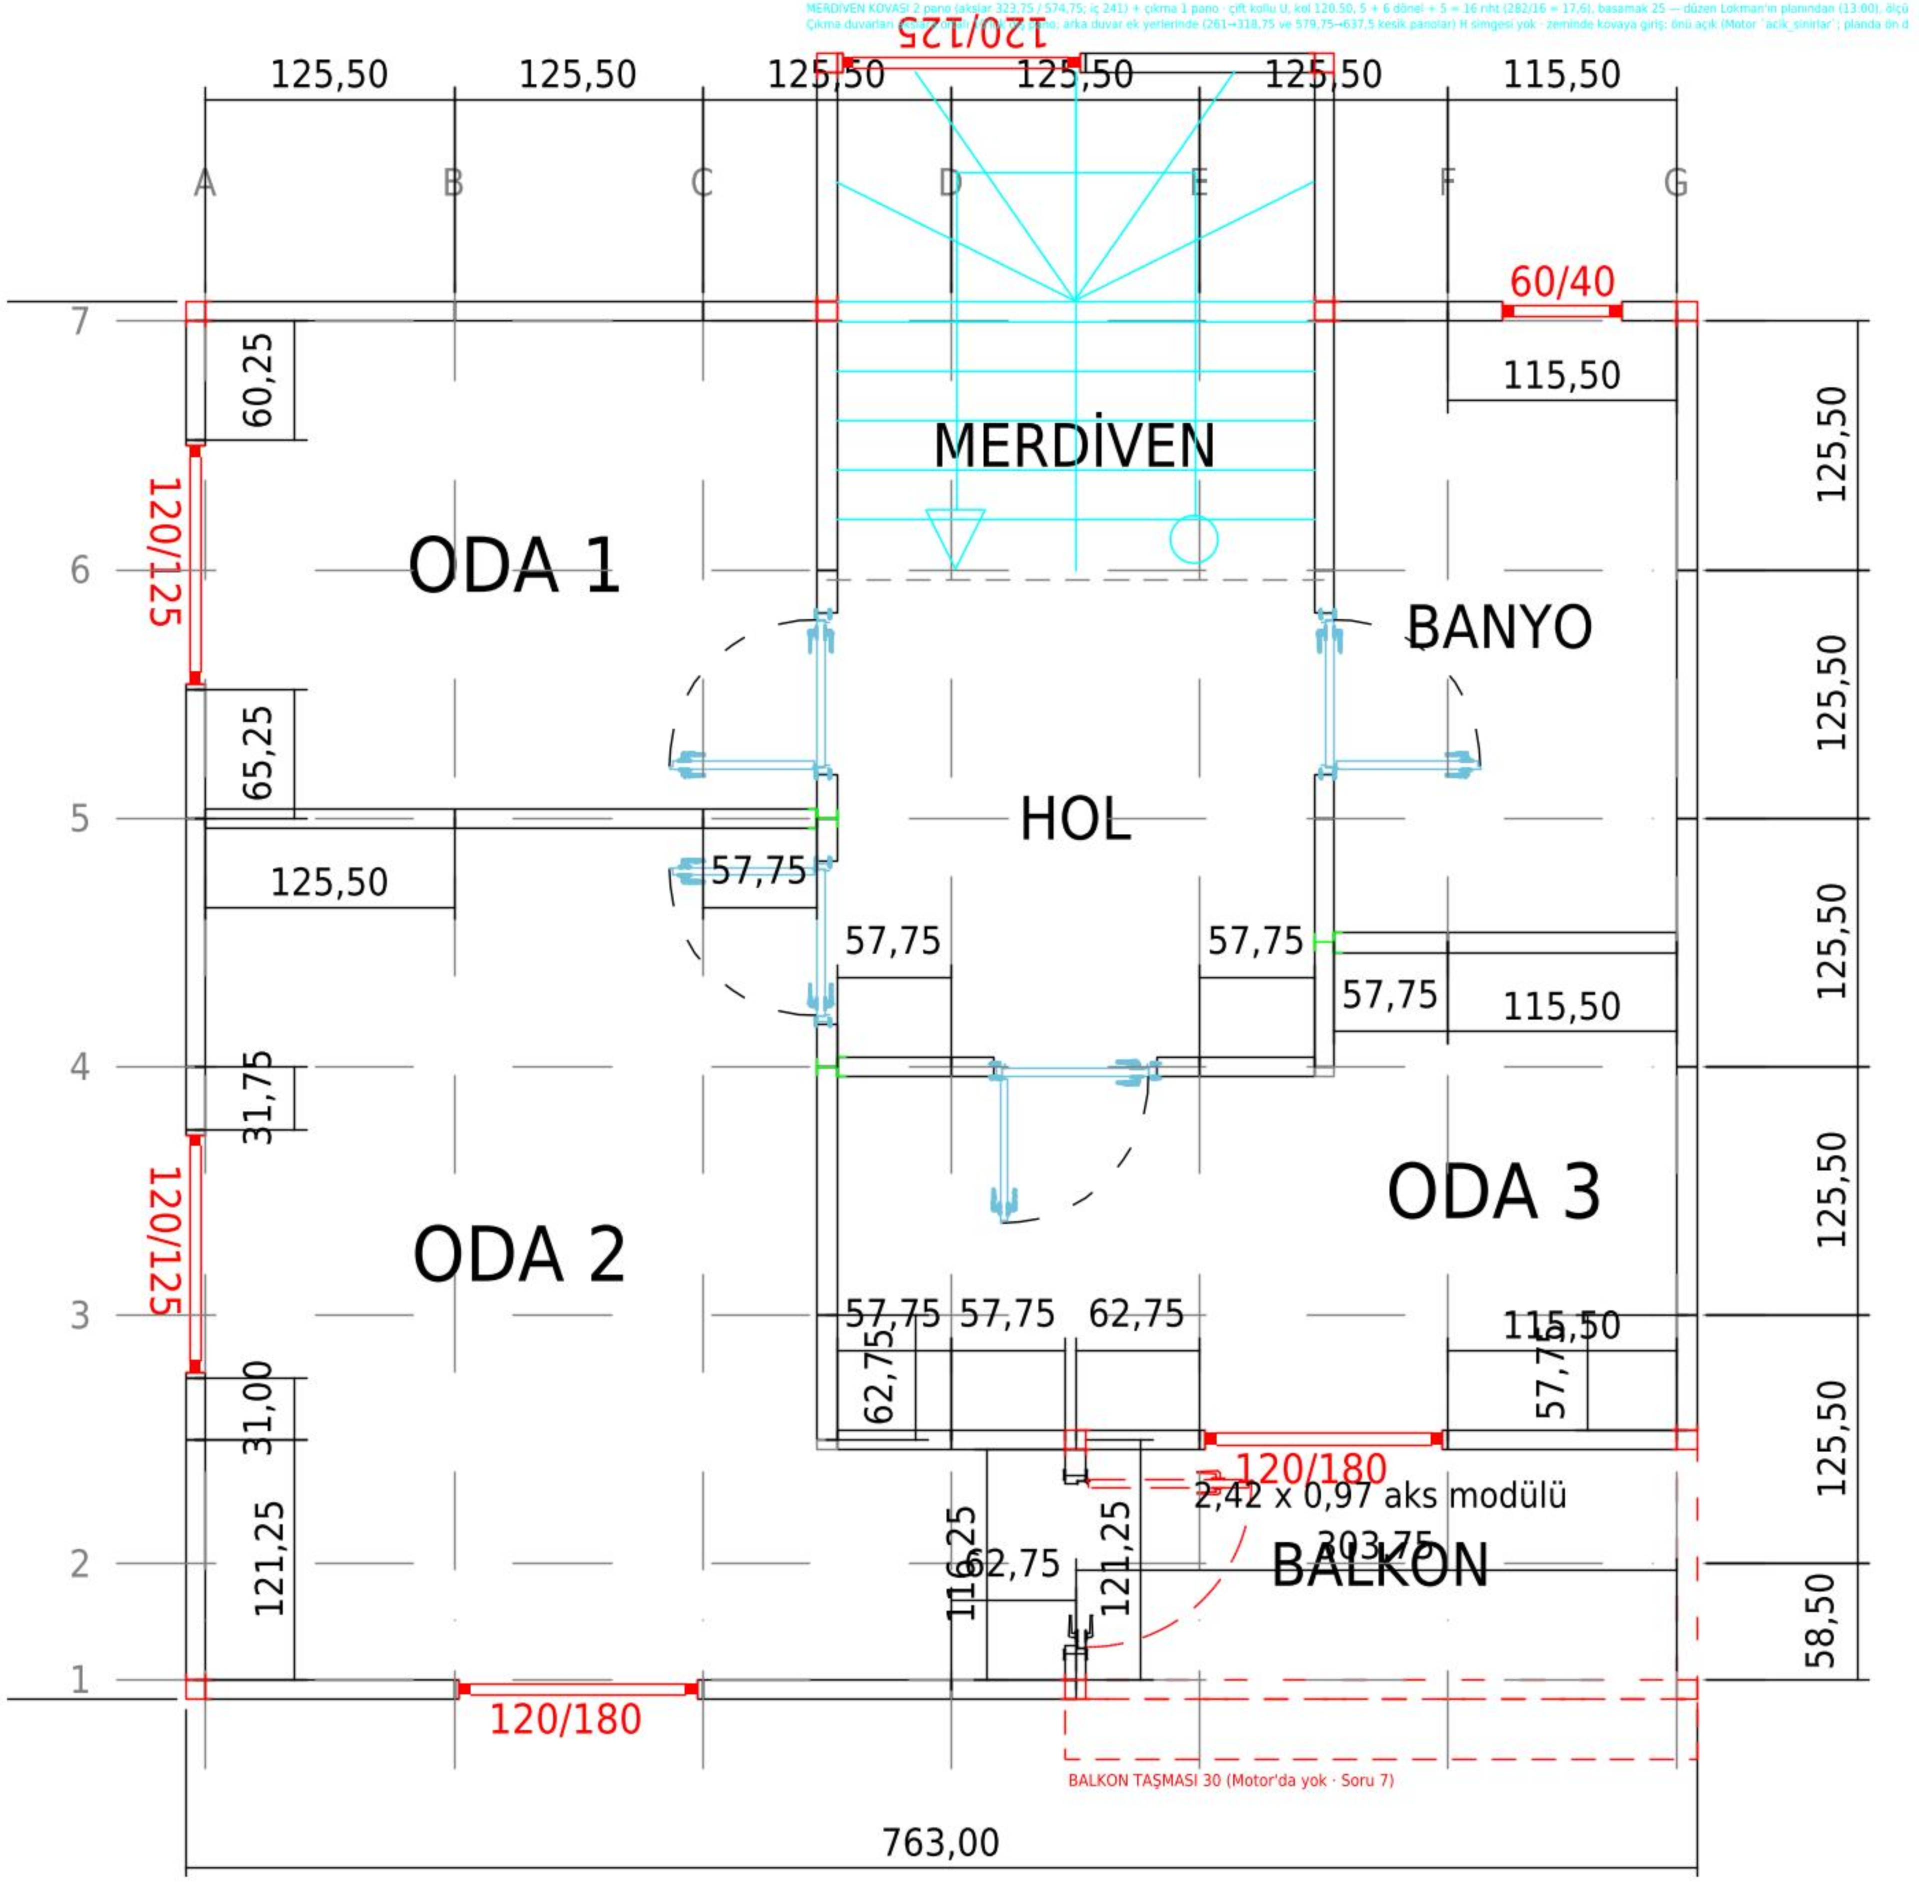
MERDİVEN KOVASI 2 pano (akslar 323,75 / 574,75; iç 241) + çıkma 1 pano · çift kollu U, kol 120.50, 5 + 6 dönel + 5 = 16 rıht (282/16 = 17,6), basamak 25 — düzen Lokman'ın planından (13:00), ölçü
Çıkma duvarları [illegible] ortalı [illegible] dış pano; arka duvar ek yerlerinde (261→318,75 ve 579,75→637,5 kesik panolar) H simgesi yok · zeminde kovaya giriş: önü açık (Motor `acik_sinirlar`; planda ön d

BALKON TAŞMASI 30 (Motor'da yok · Soru 7)

120/125
125,50
125,50
125,50
125,50
125,50
115,50
A
B
C
D
E
F
G
7
6
5
4
3
2
1
60/40
115,50
60,25
MERDİVEN
120/125
ODA 1
BANYO
65,25
HOL
125,50
57,75
57,75
57,75
57,75
115,50
31,75
ODA 3
120/125
ODA 2
57,75
57,75
62,75
115,50
62,75
57,75
31,00
120/180
2,42 x 0,97 aks modülü
121,25
116,25
62,75
121,25
303,75
BALKON
120/180
125,50
125,50
125,50
125,50
125,50
58,50
763,00

5 · Kısa kenar kesiti / kat kotları ve malzeme kartı · İE-22 CK-01 · 28.10.2026 · ölçüler cm · TASLAK

ZEMİN KAT · 763 × 706 · Şablon 2024 blok adlarıyla · İE-22 (28.10.2026)

KAT PLANI — AKSLI

n kat | 5 PANO + 115,5 cm x 5 PANO + 58,5 cm | 763 × 706 (10 + 5 × 125,5 + 115,5 + 10) cm | Model ve ölçüler: cm | 125,5 cm aks düzeni

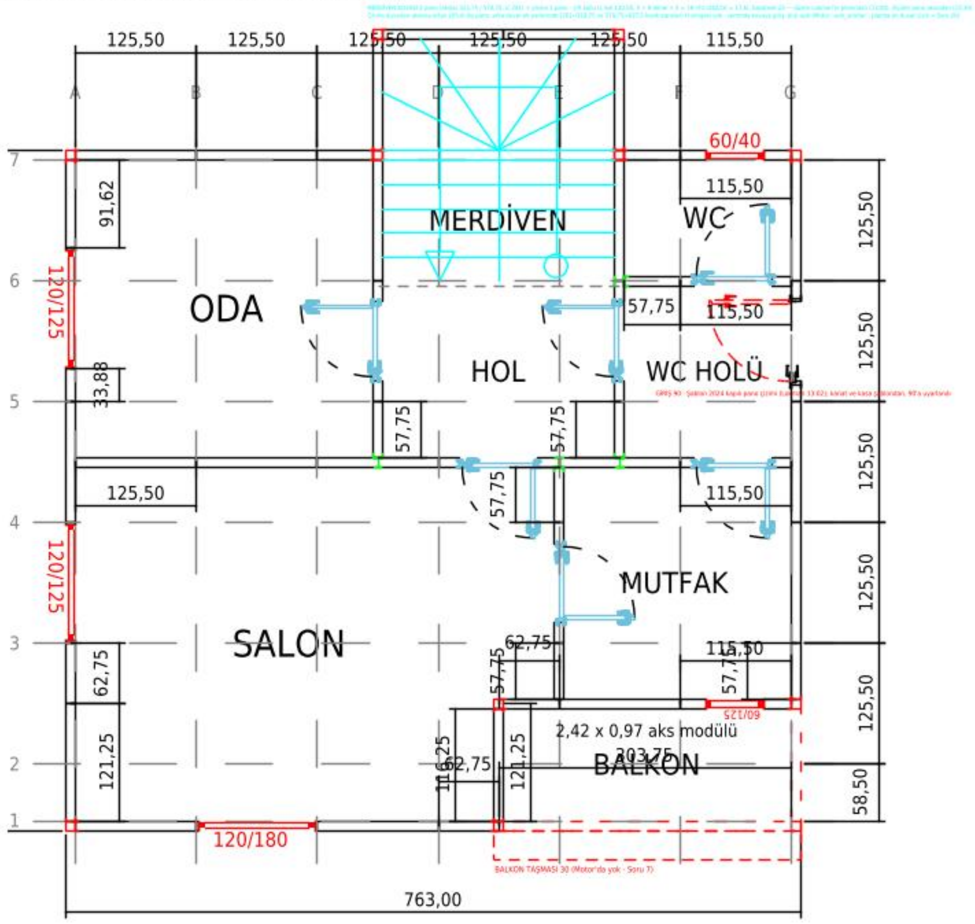
125,50
125,50
125,50
125,50
125,50
115,50
A
B
C
D
E
F
G
7
6
5
4
3
2
1
60/40
115,50
MERDİVEN
WC
91,62
120/125
ODA
HOL
57,75
115,50
WC HOLÜ
GİRİŞ 90 · Şablon 2024 kapılı pano çizimi (Lokman 13:02); kanat ve kasa şablondan, 90'a uyarlandı
33,88
57,75
57,75
125,50
57,75
115,50
120/125
MUTFAK
SALON
62,75
115,50
57,75
62,75
57,75
60/125
2,42 x 0,97 aks modülü
121,25
116,25
62,75
121,25
303,75
BALKON
120/180
BALKON TAŞMASI 30 (Motor'da yok · Soru 7)
763,00
125,50
125,50
125,50
125,50
125,50
58,50
706,00

1. KAT · 763 × 706 · Şablon 2024 blok adlarıyla · İE-22 (28.10.2026)

KAT PLANI — AKSLI

CK-01 birinci kat | 5 PANO + 115,5 cm x 5 PANO + 58,5 cm | 763 × 706 (10 + 5 × 125,5 + 115,5 + 10) cm | Model ve ölçüler: cm | 125,5 cm aks düzeni

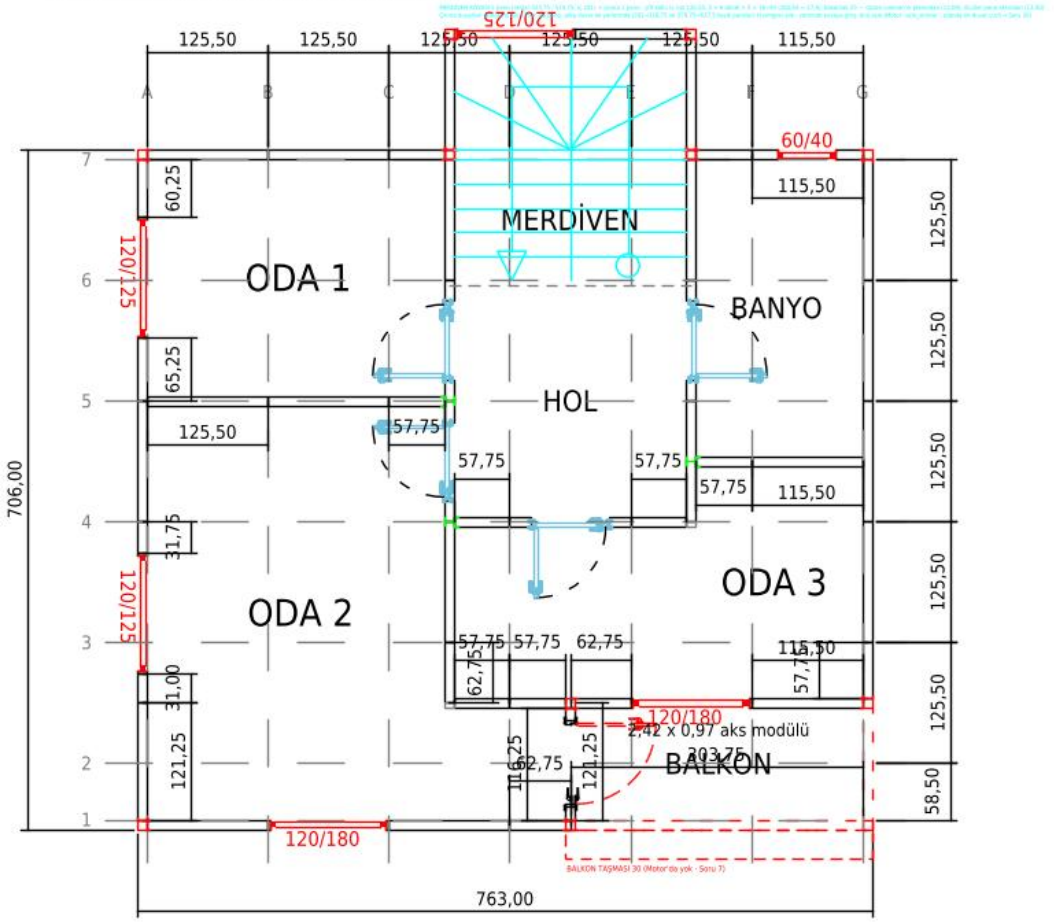
120/125
125,50
125,50
125,50
125,50
125,50
115,50
A
B
C
D
E
F
G
7
6
5
4
3
2
1
60/40
115,50
MERDİVEN
60,25
120/125
ODA 1
BANYO
65,25
HOL
125,50
57,75
57,75
57,75
57,75
115,50
31,75
120/125
ODA 2
ODA 3
57,75
57,75
62,75
115,50
62,75
57,75
31,00
120/180
2,42 x 0,97 aks modülü
121,25
116,25
62,75
121,25
303,75
BALKON
120/180
BALKON TAŞMASI 30 (Motor'da yok · Soru 7)
763,00
706,00
125,50
125,50
125,50
125,50
125,50
58,50

MALZEME KARTI — blok adı = malzeme adı (Güncel Şablon 2024 kuralı)

Blok / malzeme	ZEMİN KAT	1. KAT	Toplam	Şablon
100'LÜK 115.5'LİK (60x125) PENCERELİ PANO	1	0	1	yeni (kural)
100'LÜK 115.5'LİK (60x40) VASİSTASLI PANO	1	1	2	yeni (kural)
100'LÜK 115.5'LİK KAPILI PANO(82'LİK)	2	0	2	yeni (kural)
100'LÜK 115.5'LİK PANO	3	5	8	yeni (kural)
100'LÜK 116.25'LİK KAPILI PANO(90'LIK)	0	1	1	yeni (kural)
100'LÜK 116.25'LİK PANO	1	0	1	yeni (kural)
100'LÜK 121.25'LİK PANO	1	1	2	yeni (kural)
100'LÜK 125'LİK (120x125) PENCERELİ PANO	2	3	5	yeni (kural)
100'LÜK 125'LİK (120x180) PENCERELİ PANO	1	2	3	yeni (kural)
100'LÜK 125'LİK KAPILI PANO(82'LİK)	4	4	8	yeni (kural)
100'LÜK 125'LİK KAPILI PANO(90'LIK)	1	0	1	yeni (kural)
100'LÜK 125'LİK PANO	16	15	31	var
100'LÜK 31'LİK PANO	0	1	1	yeni (kural)
100'LÜK 31.75'LİK PANO	0	1	1	yeni (kural)
100'LÜK 33.88'LİK PANO	1	0	1	yeni (kural)
100'LÜK 57.75'LİK PANO	8	9	17	yeni (kural)
100'LÜK 60.25'LİK PANO	0	1	1	yeni (kural)
100'LÜK 62.75'LİK PANO	3	3	6	yeni (kural)
100'LÜK 65.25'LİK PANO	0	1	1	yeni (kural)
100'LÜK 91.62'LİK PANO	1	0	1	yeni (kural)
100'LÜK VERANDA PROFİLİ 126.25 (YAN)	1	1	2	yeni
100'LÜK VERANDA PROFİLİ 303.75 (ÖN)	1	1	2	yeni
100X100 3 LÜ H BAĞLANTI DİREĞİ	4	3	7	var
100X100 VERANDA DİKMESİ	1	1	2	yeni
2X100X100 İÇ KÖŞE DİREĞİ	0	2	2	var

ORTAK: 100X100 DIŞ KÖŞE DİREĞİ (şablon bloğu; kutu profil, sürekli iki kat boyu 5320 R02) — kat kat sayılmaz: 6 gövde köşesi + 2 çıkma arka köşesi + 2 çıkma-gövde birleşimi (Lokman 13:57) = 10

Not: kapı panellerde [SAĞ ÜST] vb. ek kanat yönüdür, malzeme adına girmez. 'yeni (kural)' = şablonda yok, şablonun ad kuralıyla türetildi.

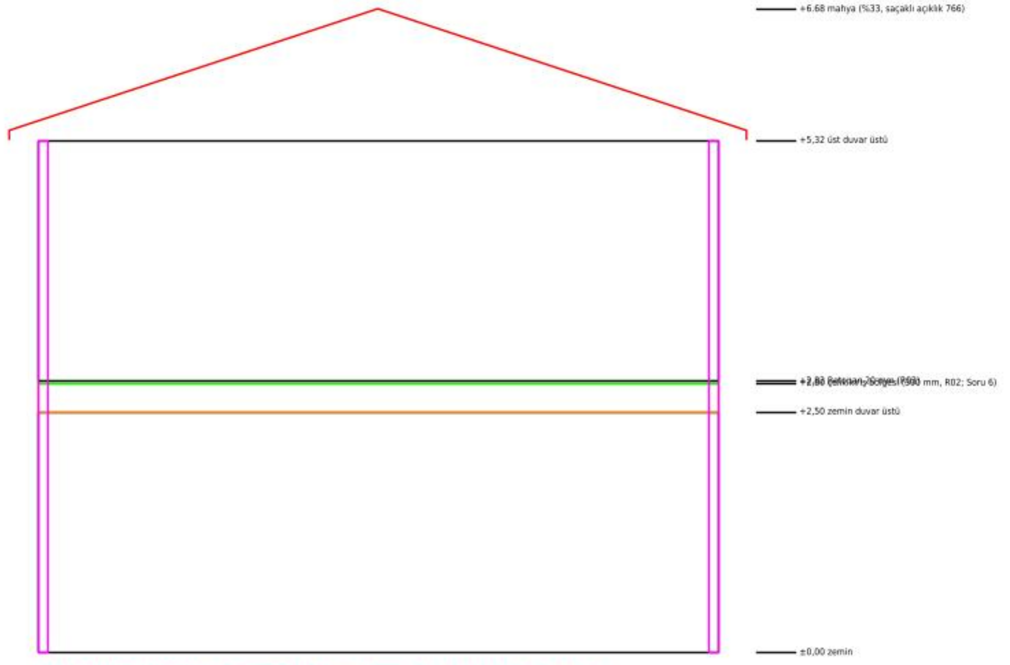
+6.68 mahya (%33, saçaklı açıklık 766)
+5,32 üst duvar üstü
+2,82 [illegible]
+2,80 [illegible] mm, R02; Soru 6)
+2,50 zemin duvar üstü
±0,00 zemin

KISA KENAR KESİTİ / KAT KOTLARI — döşeme tek katla aynı (Lokman 28.10); ara kat R02 verisi, kural değil

Köşe direkleri 100×100 sürekli, iki kat boyu (Lokman 28.10 12:09; R02 100×100×5320; et kalınlığı Soru 8)