
İki bağımsız daire • Ortak kat planı

Zemin +0 mm / Üst kat +2820 mm | Her kat 75,00 m² brüt | Ölçek 1:50

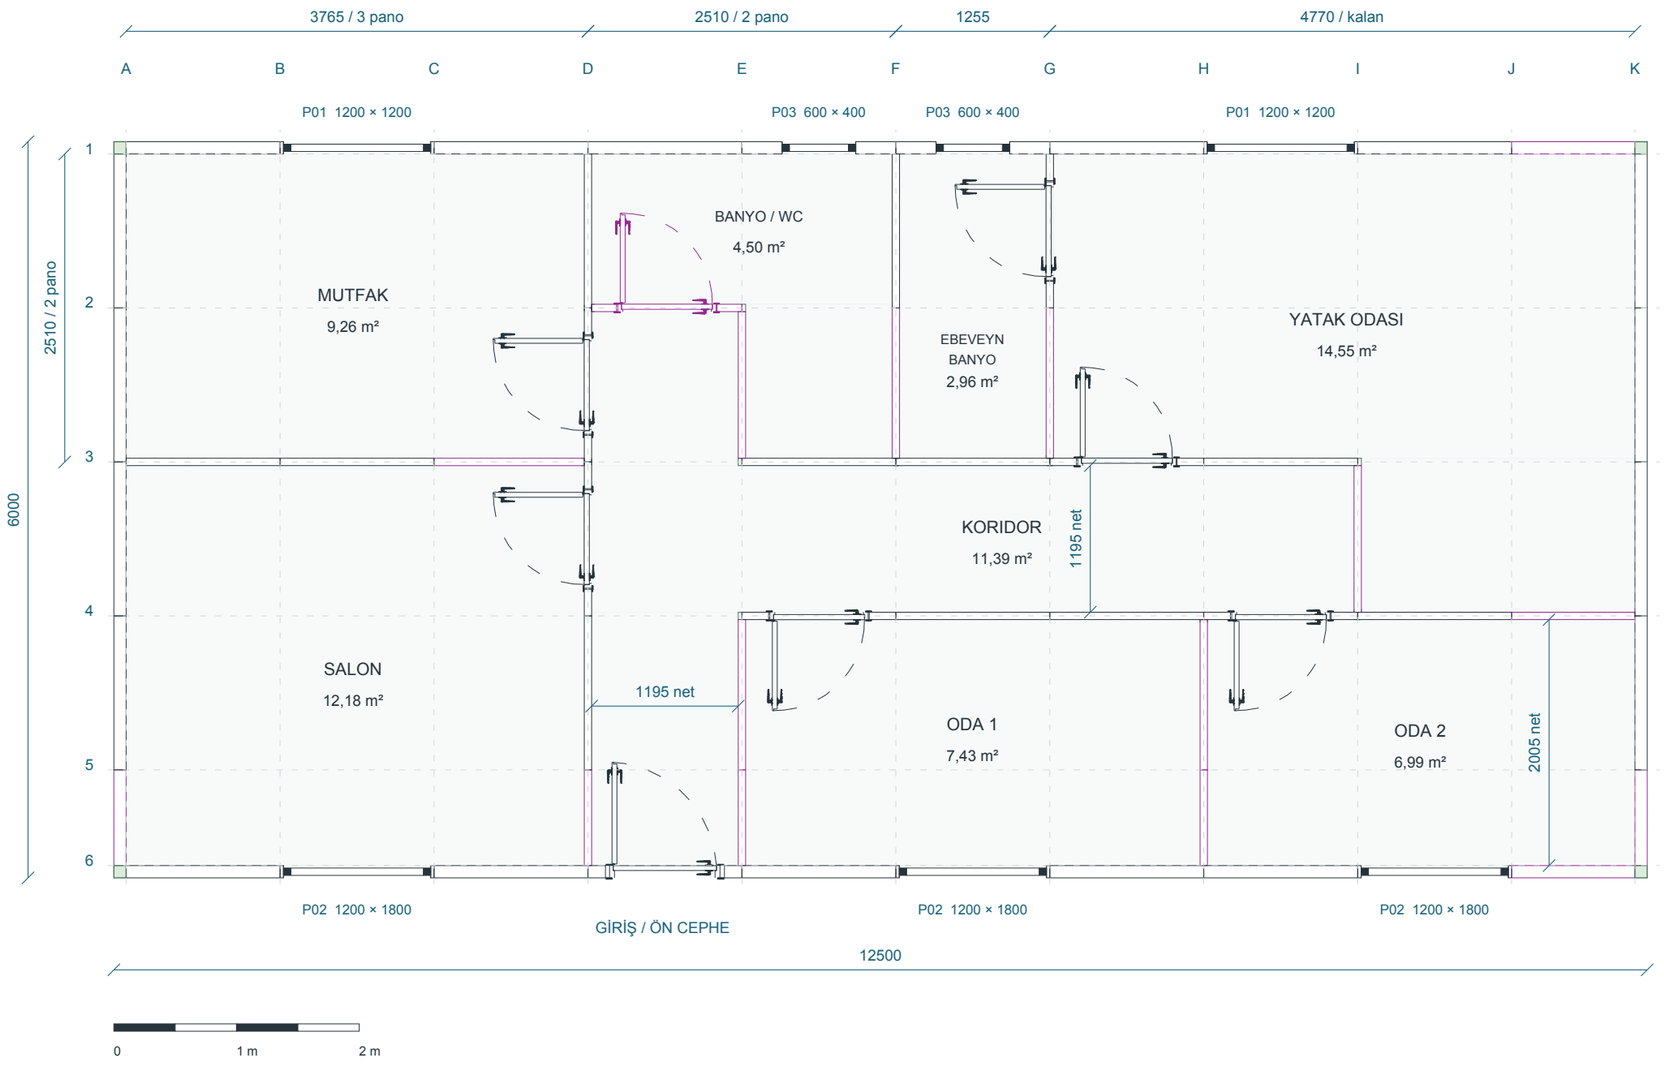

AKS YERLEŞİMİ

Mutfak: 3 × 2 modül

3765 × 2510 mm aks ölçüsü

Banyo: 2 modül genişlik

Ebeveyn banyo: 1 modül

Koridor: 1255 − 30 − 30

1195 mm net genişlik

Banyo giriş kademesi:

1 × 1 modül (1255 × 1255)

NET ALANLAR

Mutfak	9,26 m²
Salon	12,18 m²
Banyo / WC	4,50 m²
Ebeveyn banyo	2,96 m²
Yatak odası	14,55 m²
Oda 1	7,43 m²
Oda 2	6,99 m²
Koridor	11,39 m²
Toplam / kat	**69,27 m²**

Duvarlar ve kapı eşikleri hariç.

UYGULANAN MODÜLER DÖNÜŞÜM

İç akslar sol üstten 1255 mm aralıklarla ilerler; dış ölçü 12500 × 6000 mm kalır.


Fotoğraftaki yuvarlak oda ölçüleri pano adedine çevrildi. Son boy farkları sağ ve alt bitişlerde bırakıldı.

Ön odaların net derinliği 2005 mm oldu. Ebeveyn banyo kapısı yatak odası tarafından çözüldü.

Balkon ve merdiven bu projeden çıkarıldı; katlara girişler bağımsızdır.

Pano montaj planı

Her kat için aynı yerleşim | PN001–PN059 | Standart pano 1255 mm | Ölçek 1:50

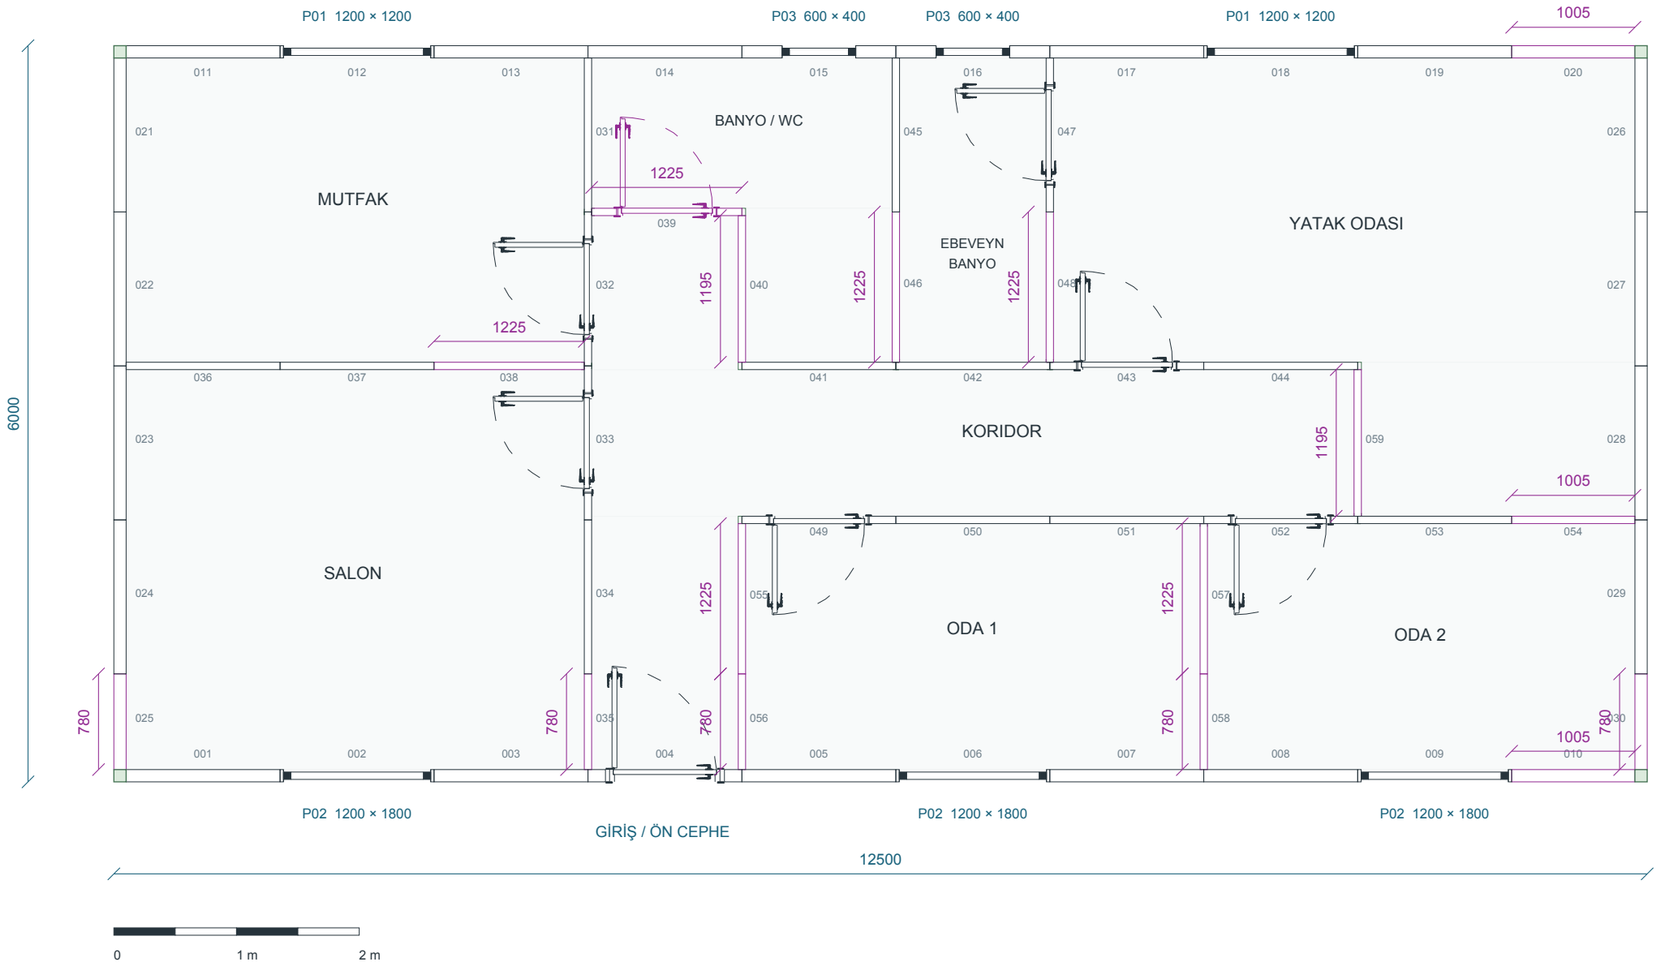

BİR KATTA

30 dış pano

29 iç pano

6 üçlü H bağlantı

4 iç köşe bağlantısı

7 pencere / 8 kapı

ÖLÇÜ RENKLERİ

Mor: standart dışı pano boyu

Yeşil: birleşim / köşe

Gri 001…059: pano numarası

Dış panolarda son kalanlar:

Uzun kenar → 1005 mm

Kısa kenar → 780 mm

İçte 30 mm indirimler yalnız birleşimin yüzünde yapılır. Aks çizgisi yer değiştirmez.

CEPHE TOPLAM KONTROLLERİ • HER KAT

Ön / Arka: 100 + 9 × 1255 + 1005 + 100 = 12500 mm

Sol / Sağ: 100 + 4 × 1255 + 780 + 100 = 6000 mm

Kapılı / pencereli pano açıklığıyla birlikte tek pano sayılır. Doğrama ayrıca sayılır.

Dört dış köşenin her birinde tek sürekli 100 × 100 × 5320 mm profil bulunur.


Ön görünüş ve kat kotları

300 mm ara kat çelik bölgesi + 20 mm Betopan | Sürekli dış köşe kolonları | Ölçek 1:50

ÖN CEPHE / 1:50



KAT KOTLARI / 1:66,67

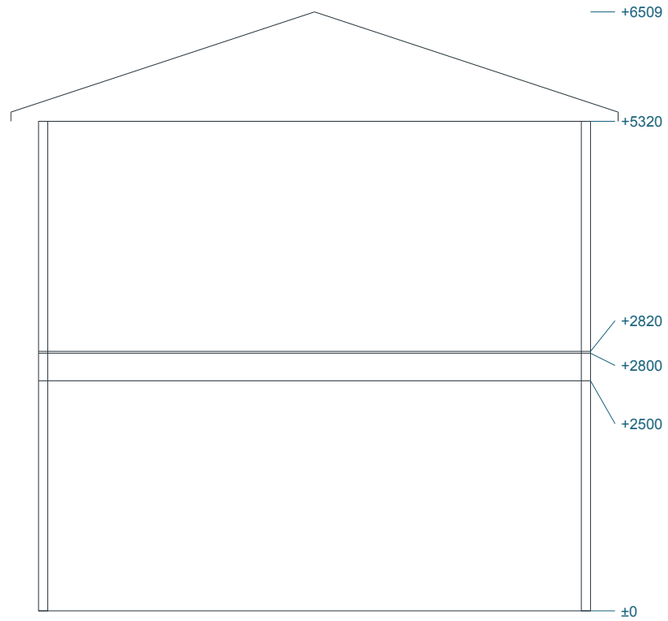

100 × 100 × 5320

4 adet sürekli köşe profili

DÜŞEY DİZİLİM

0–2500: zemin kat duvarları • 2500–2800: çelik kiriş bölgesi

2800–2820: 20 mm Betopan • 2820–5320: üst kat duvarları

P02 pencere alt kotları +200 / +3020 mm; pencere yüksekliği 1800 mm; lento 500 mm.

Çatı çizgisi mevcut %33, 300 mm saçak ve 100 mm topuk kuralıyla gösterildi.

TANIMLI OLMAYAN ÜRÜN BİLGİLERİ

Kapı üst kotu 2000 mm çizim kabulüdür. Kapı ürün yüksekliği ve H / iç köşe profil kesim boyları katalogda yoktur.

Çelik bölge gösterimi, kiriş kesit ve adet projesi değildir. Betopan 74,96 m² geometrik alandır; levha kesim planı değildir.