
ZEMİN KAT — yalnız dış ölçüler (dış yüzden dış yüze, cm) · İE-22 CK-01 · 28.10.2026 · TASLAK

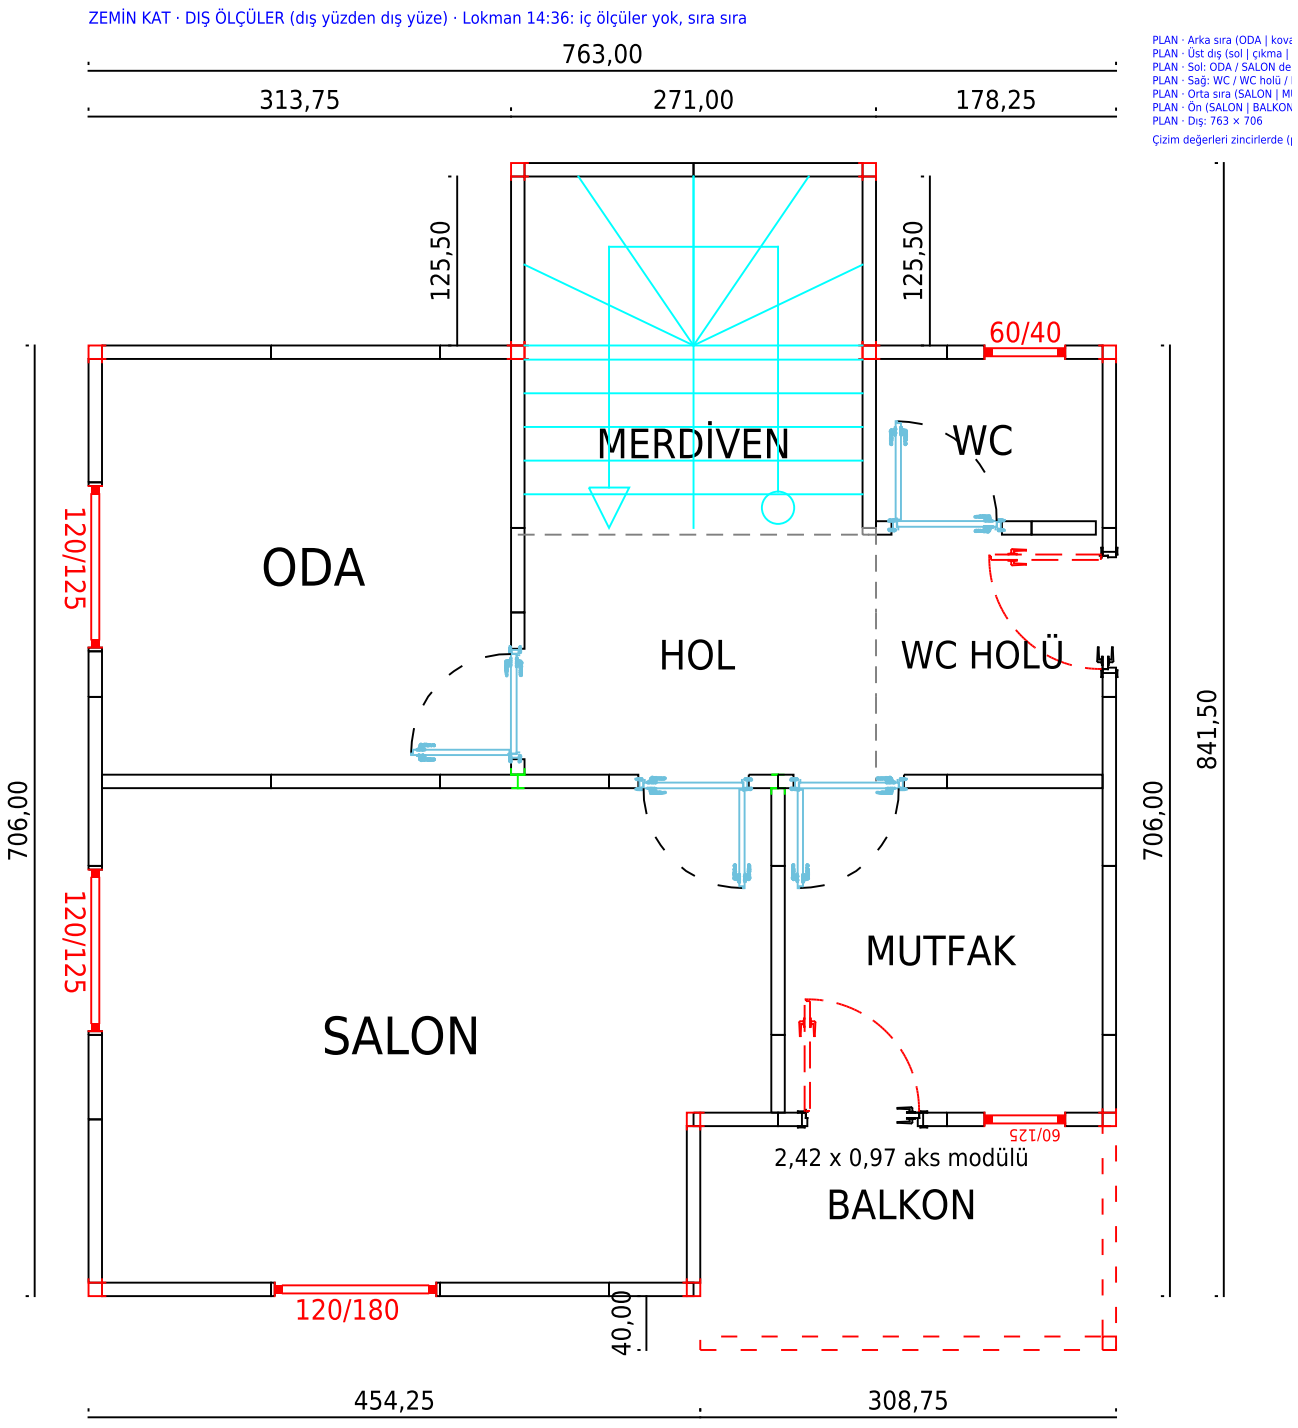

KAT PLANI — AKSLI

01 zemin kat | 5 PANO + 115,5 cm x 5 PANO + 58,5 cm | 763 × 706 (10 + 5 × 125,5 + 115,5 + 10) cm | Model ve ölçüler: cm | 125,5 cm aks düzer

