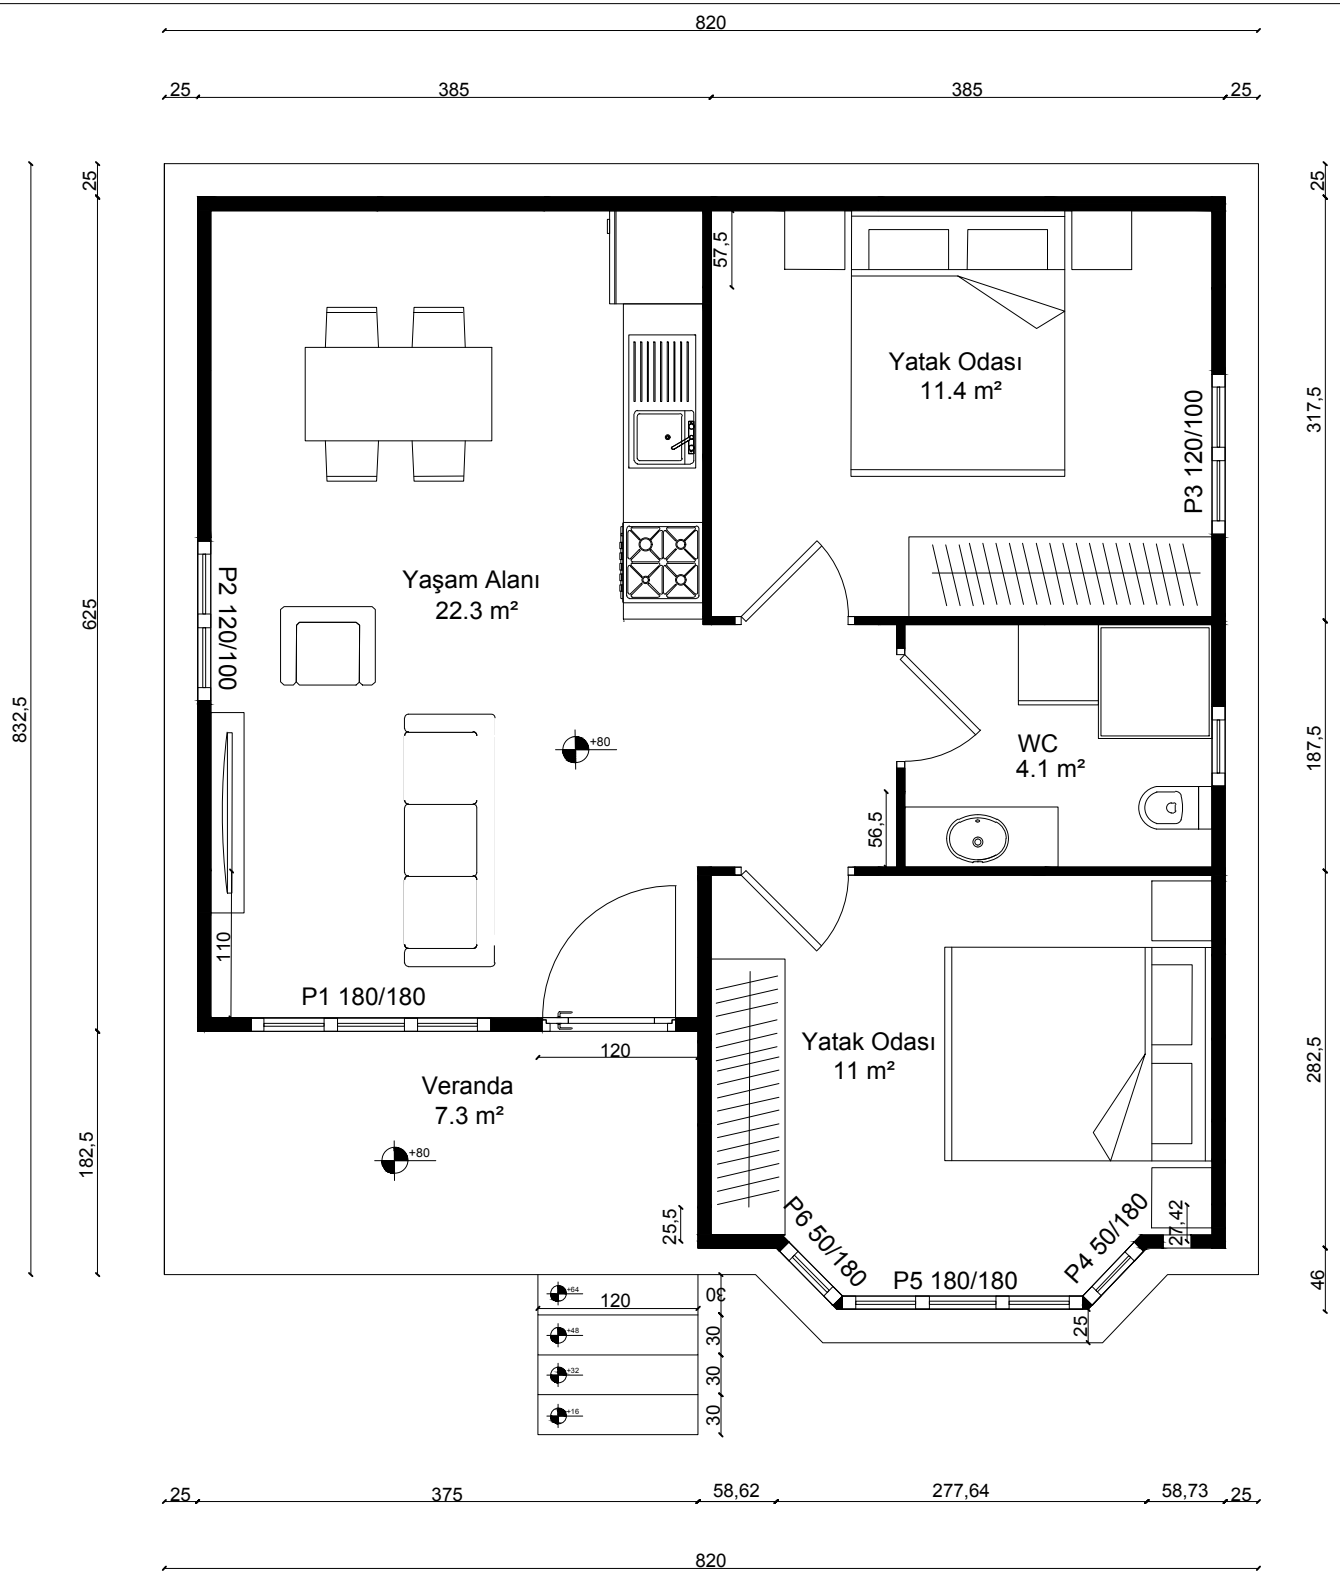
820
25
385
385
25
832,5
25
625
182,5
25
317,5
187,5
282,5
46
57,5
Yatak Odası
11.4 m²
P3 120/100
P2 120/100
Yaşam Alanı
22.3 m²
+80
WC
4.1 m²
56,5
110
P1 180/180
120
Yatak Odası
11 m²
Veranda
7.3 m²
+80
25,5
P6 50/180
P5 180/180
P4 50/180
27,42
25
120
+64
+48
+32
+16
0
30
30
30
25
375
58,62
277,64
58,73
25
820