
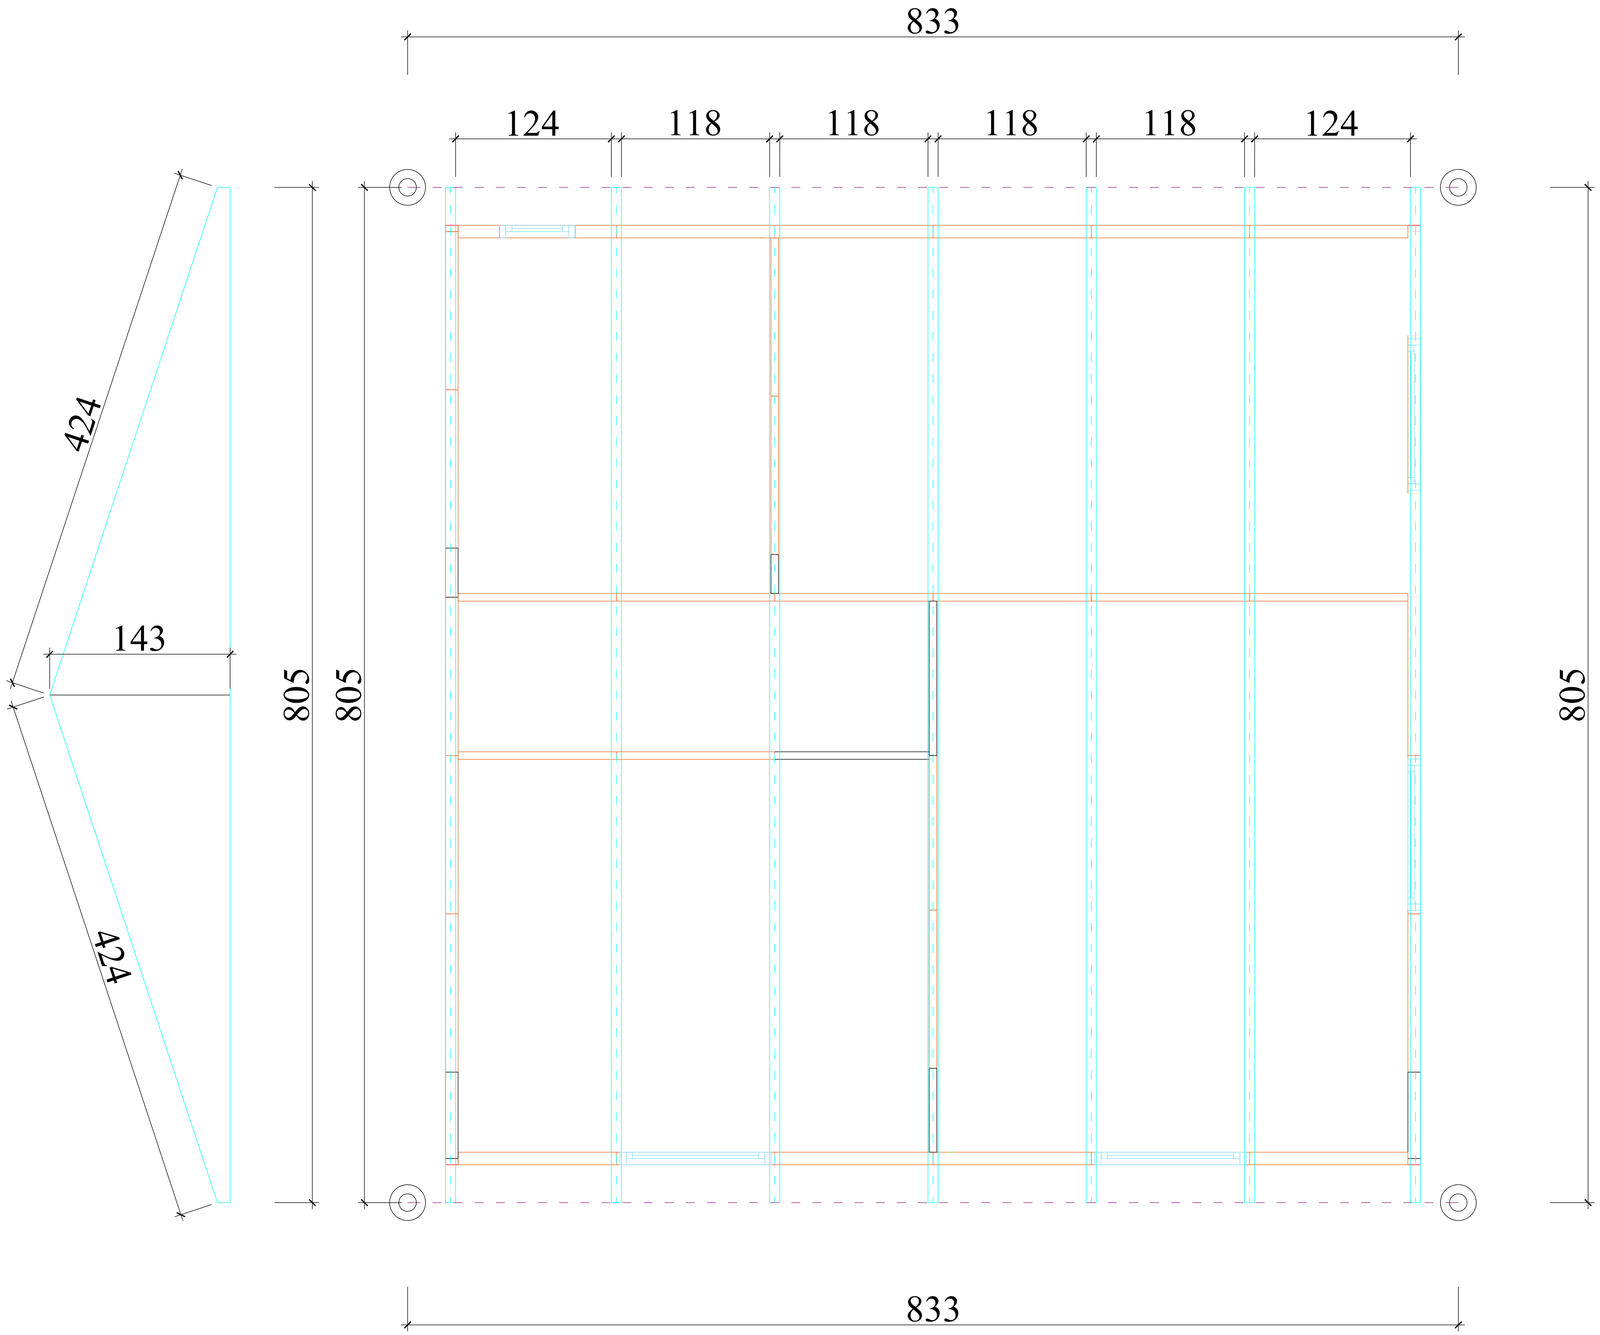


MAKAS VE DERE YERLEŞİM PLANI

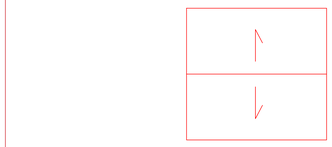


ÇATI ŞEKLİ

1-) Aşıklar 60 cm aralıklarla monte edilecektir

2-) Mahya aşığı 20 cm de monte edilecektir

MONTAJ DETAYLARI

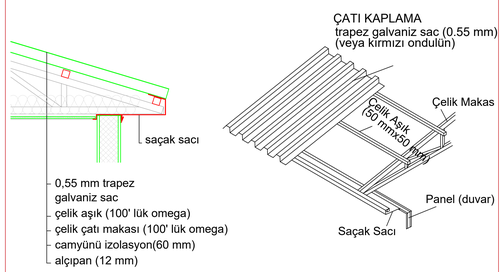

Çatı Detayı

Çatı Detayı

ÇATI DETAYLARI

Satış Temsilcisi		ÇİZEN	

LOFTEV