
TEKNİK ÖZELLİKLER


Bina Yüksekliği	2500 mm
Dış Duvarlar	100 mm
İç Duvarlar	60 mm
Panel Türü	Pres Panel
Çatı Şekli	Dörtomuz Çatı
Çatı Kaplaması	Sandviç Panel
Çatı Kaplama Rengi	Antrasit Gri
Dış Kapı	Çelik Standart
İç Kapılar	Standart Amerikan
Dış Cephe Boya	Jotun 1140 - SAND
İç Cephe Boya	Polisan Cİ-6610 / Yeni Kuğu
Pencere Rengi	ANTRASİT
Tavan	Düz
Saçak ve Alın Rengi	Antrasit Gri


AÇIKLAMA


1- Dere tam boy olacak.
2- Vitrifiye grubu alıcıya ait.
3- Banyo içleri boardex olacak.
4- Veranda tavan boardex olacak.
5- Çatı izolasyonu Kanuf mineral yün olacaktır.

MODERN PREFABRIK 140M2 PENCERE DETAY

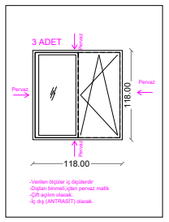


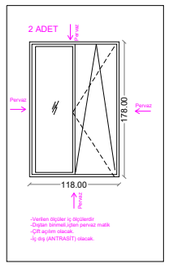


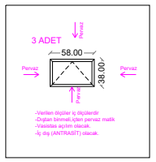

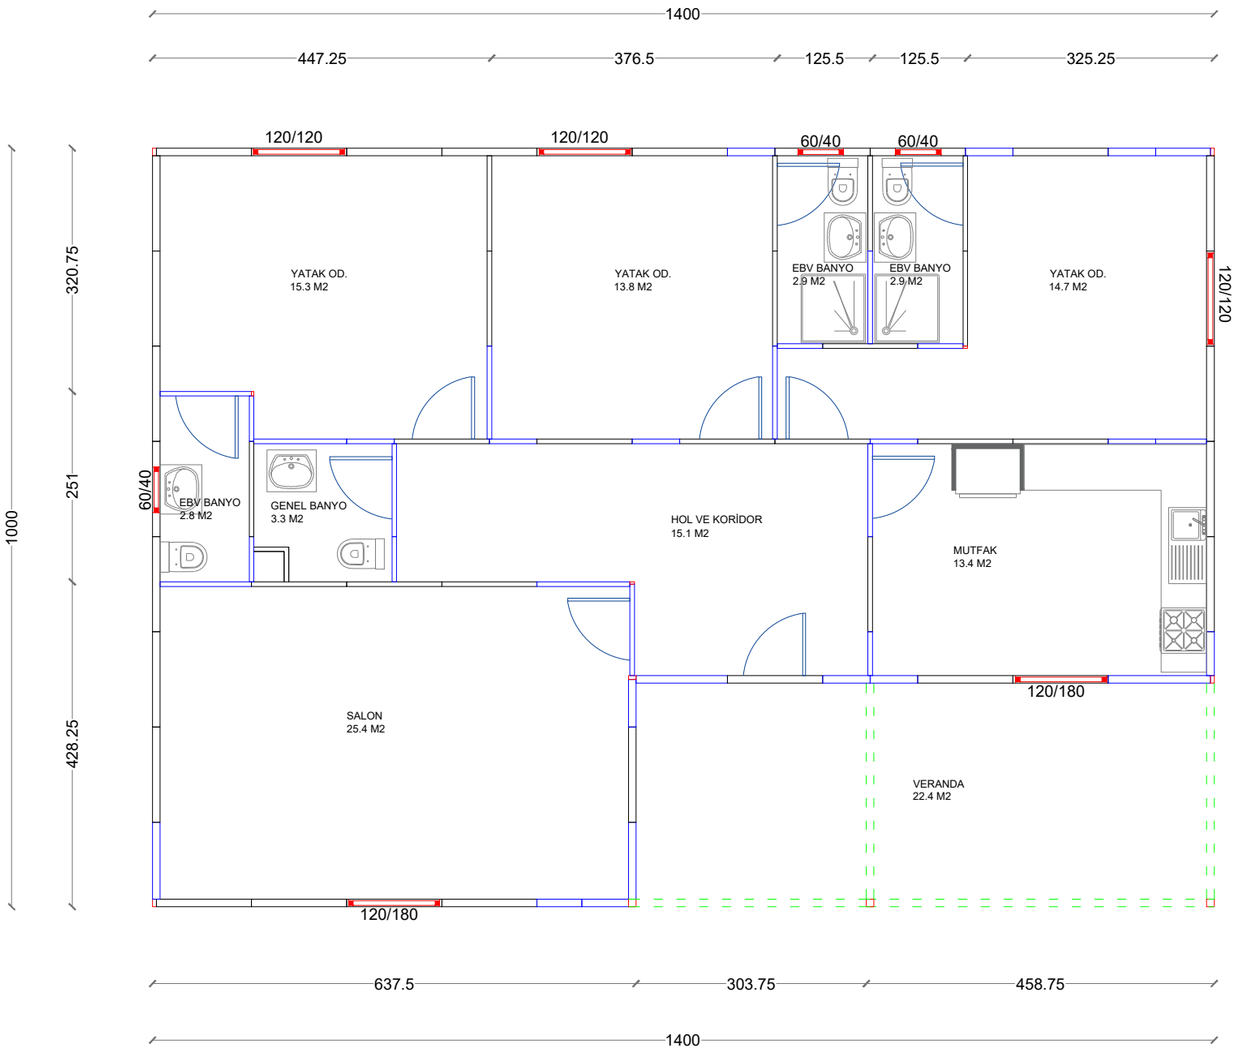


MODERN PREFABRIK 140 m² PREFABRİK KONUT	
ÇİZEN	Ubeydullah Özer
KONTROL EDEN	Lokman Sayım

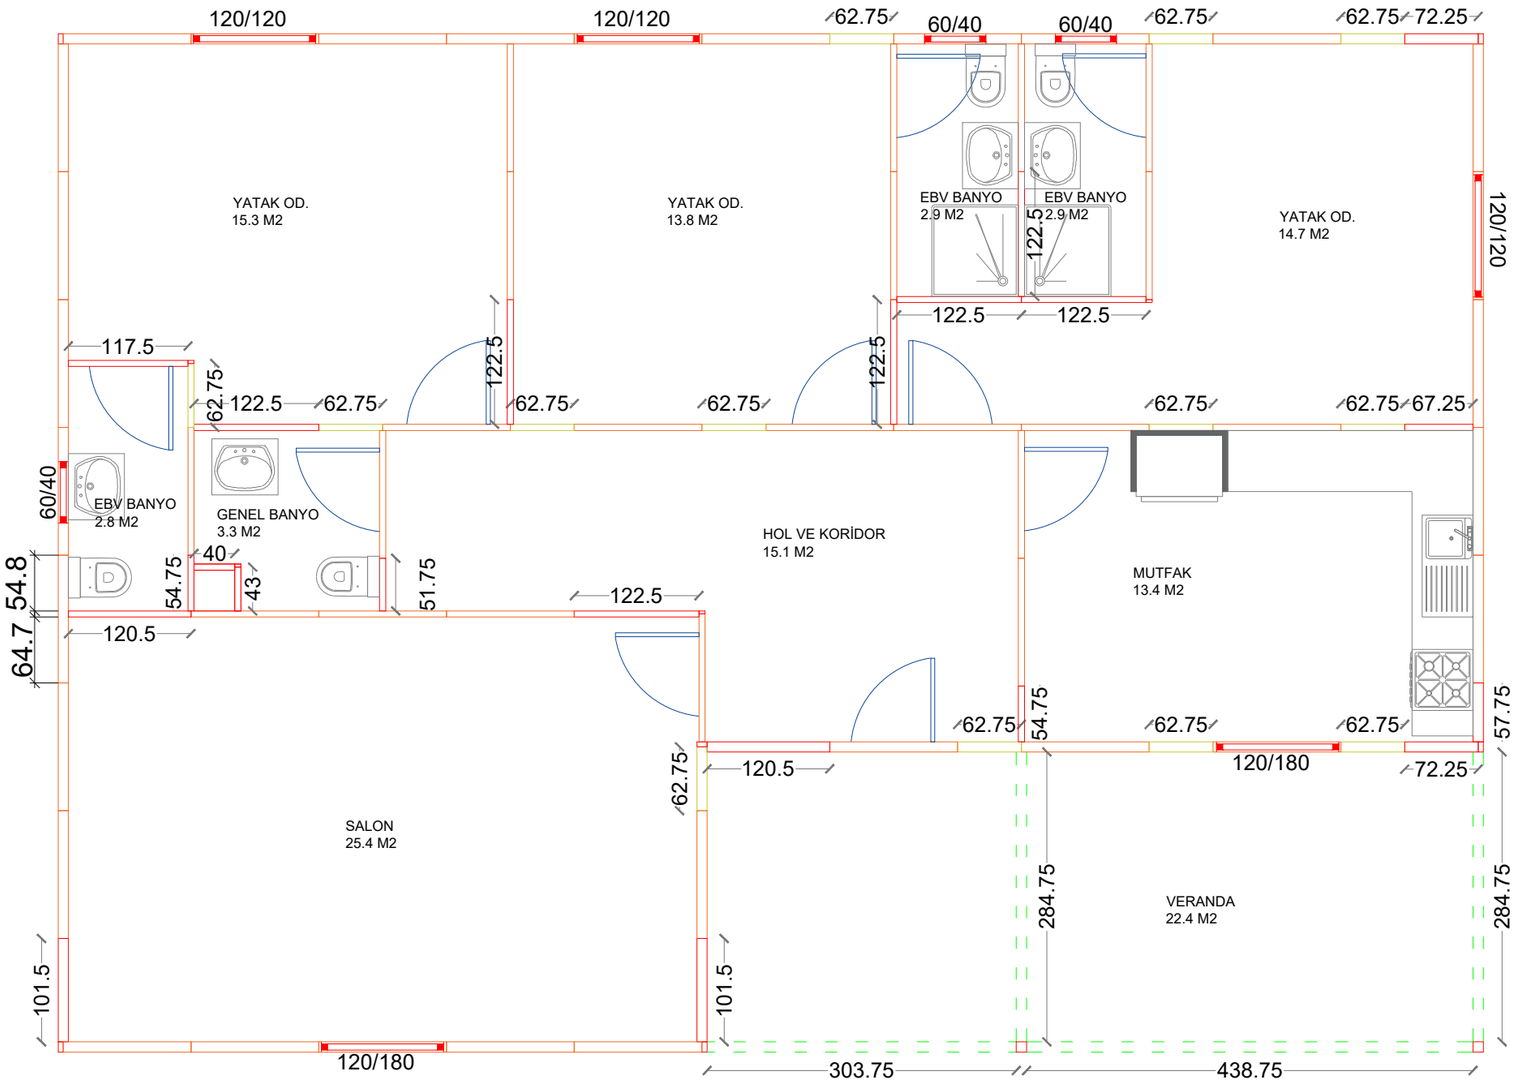

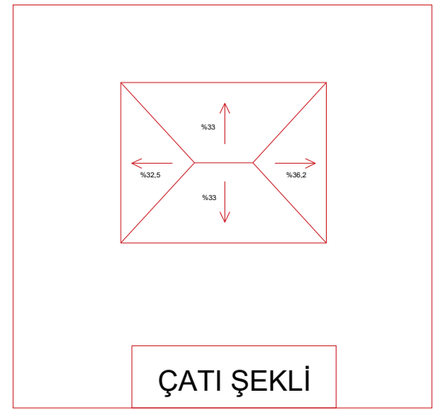


MONTAJ PLANI

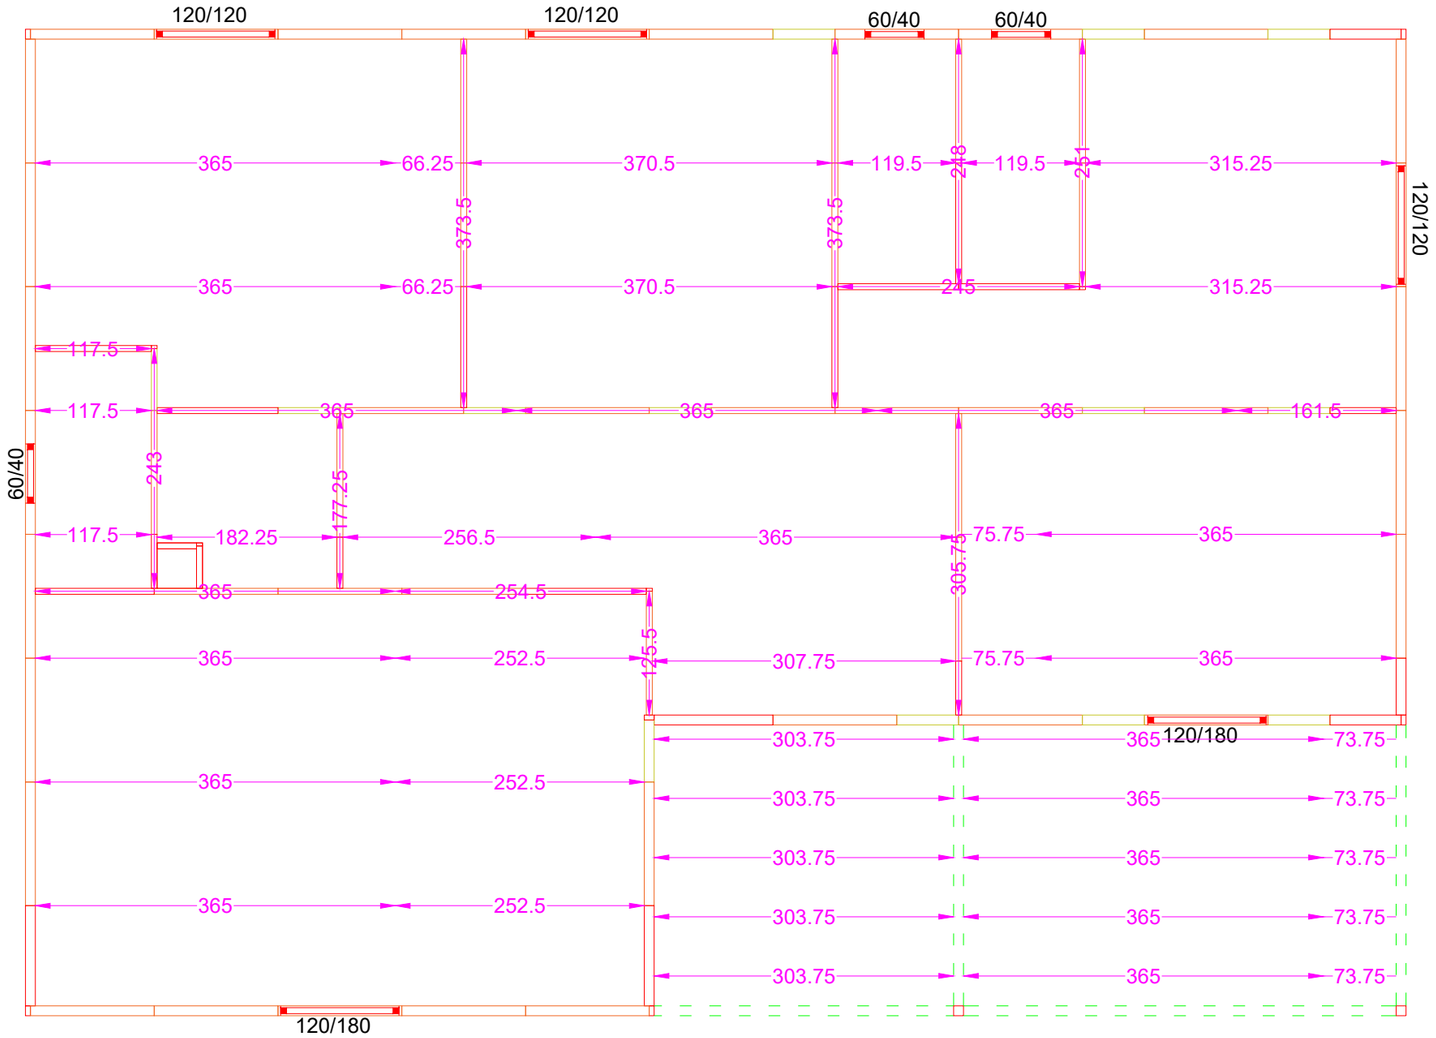

1-) Veranda içi ters tavan yapılacak
(Omega profiller 60 cm de bir monte edilecek)

2-) Diğer mahaller asma tavan yapılacak
(Omega profiller 125 cm de bir monte edilecek)


MONTAJ DETAYLARI

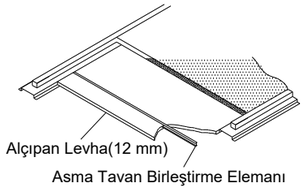

TAVAN OMEGA YERLEŞİM PLANI

H (DÜBELLİ & KULAKLI)	*H* (DÜBELLİ)	*H* (STANDART)	*3'LÜ H* (DÜBELLİ & KULAKLI)	*3'LÜ H* (DÜBELLİ)	*3'LÜ H* (STANDART)














	H (DÜBELLİ&KULAKLI) 100*100*2500	*Dış Duvarlarda Çatı Makaslarına denk gelen H'lardır.*
	H (DÜBELLİ) 100*100*2500	*Dış Duvarlarda Çatı Makaslarının denk gelmediği ve çatı makasının düz oturduğu H'lardır.*
	H (STANDART) 60*60*2500	*İç Duvarlarda kullanılan H'lardır.*
	3'LÜ H (DÜBELLİ & KULAKLI) 100*100*60*2500	*Dış Duvarlarda Çatı Makaslarının 3'lü duvar birleşimlerine denk geldiği H'lardır.*
	3'LÜ H (DÜBELLİ) 100*100*60*2500	*Dış Duvarlarda Çatı Makaslarının 3'lü duvar birleşimlerine denk gelmediği H'lardır.*
	3'LÜ H (STANDART) 60*60*2500	*İç Duvarlarda Çatı Makaslarının 3'lü duvar birleşimlerine denk geldiği H'lardır.*

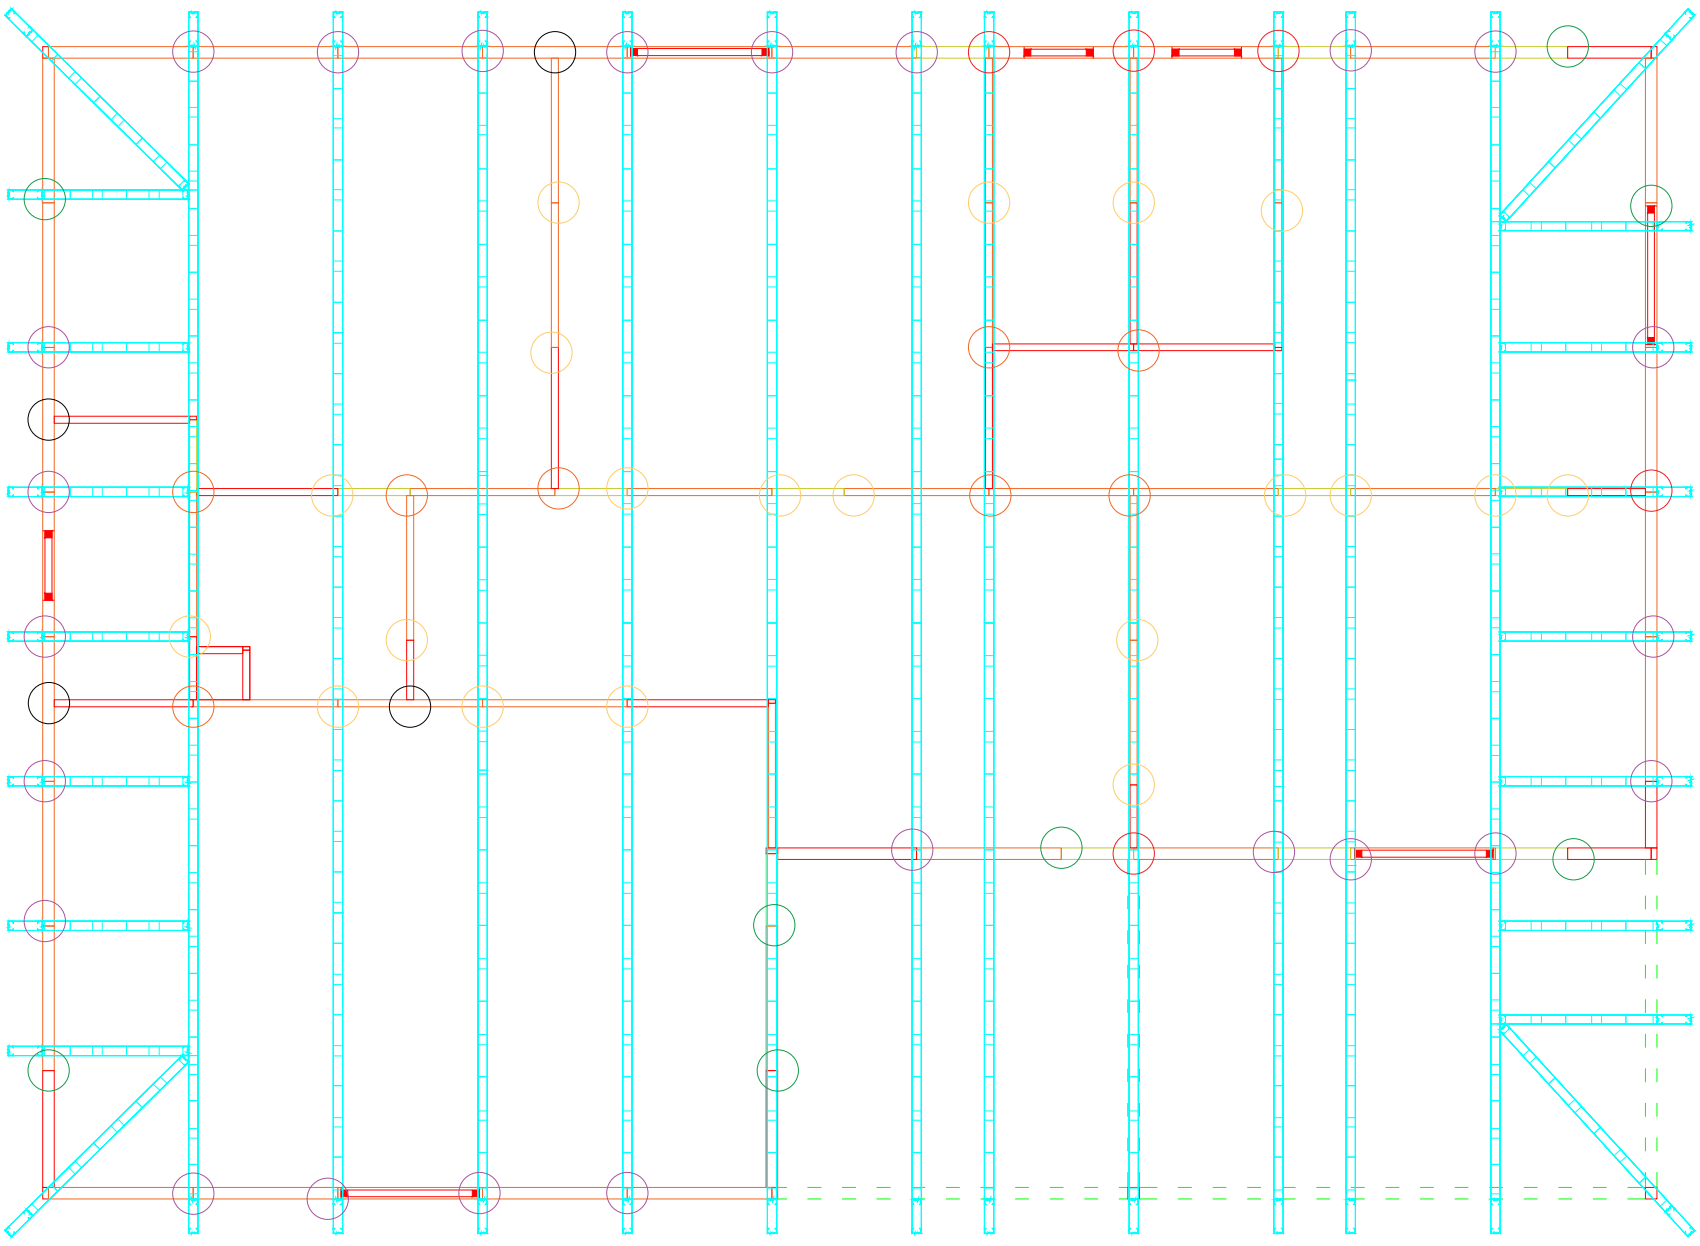


H YERLEŞİM PLANI


ÖZEL KUTU PROFİL VE H KAYNAK DETAYLARI


PROJE: MODERN PREFABRIK 140 M2

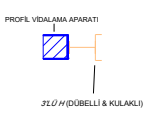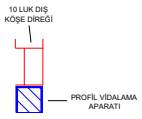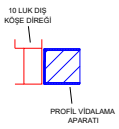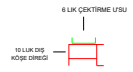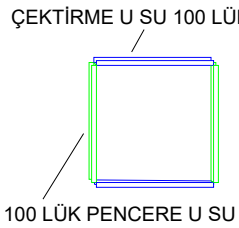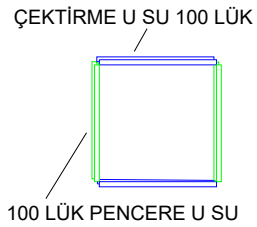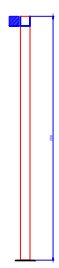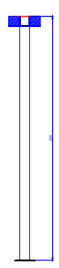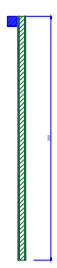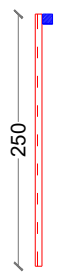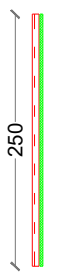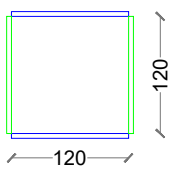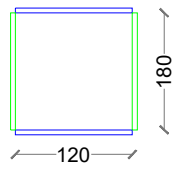A	B	C	D	E	F	G	H
ADET: 1 KALINLIK: 3MM	ADET: 1 KALINLIK: 3MM	ADET: 1 KALINLIK: 3MM	ADET: 1 KALINLIK: STANDART	ADET: 1 KALINLIK: STANDART	ADET: 1 KALINLIK: STANDART	ADET: 3 KALINLIK: STANDART	ADET: 2 KALINLIK: STANDART
							
							


ÖZEL KAYNAKLI PROFILLER MONTAJ PLANI

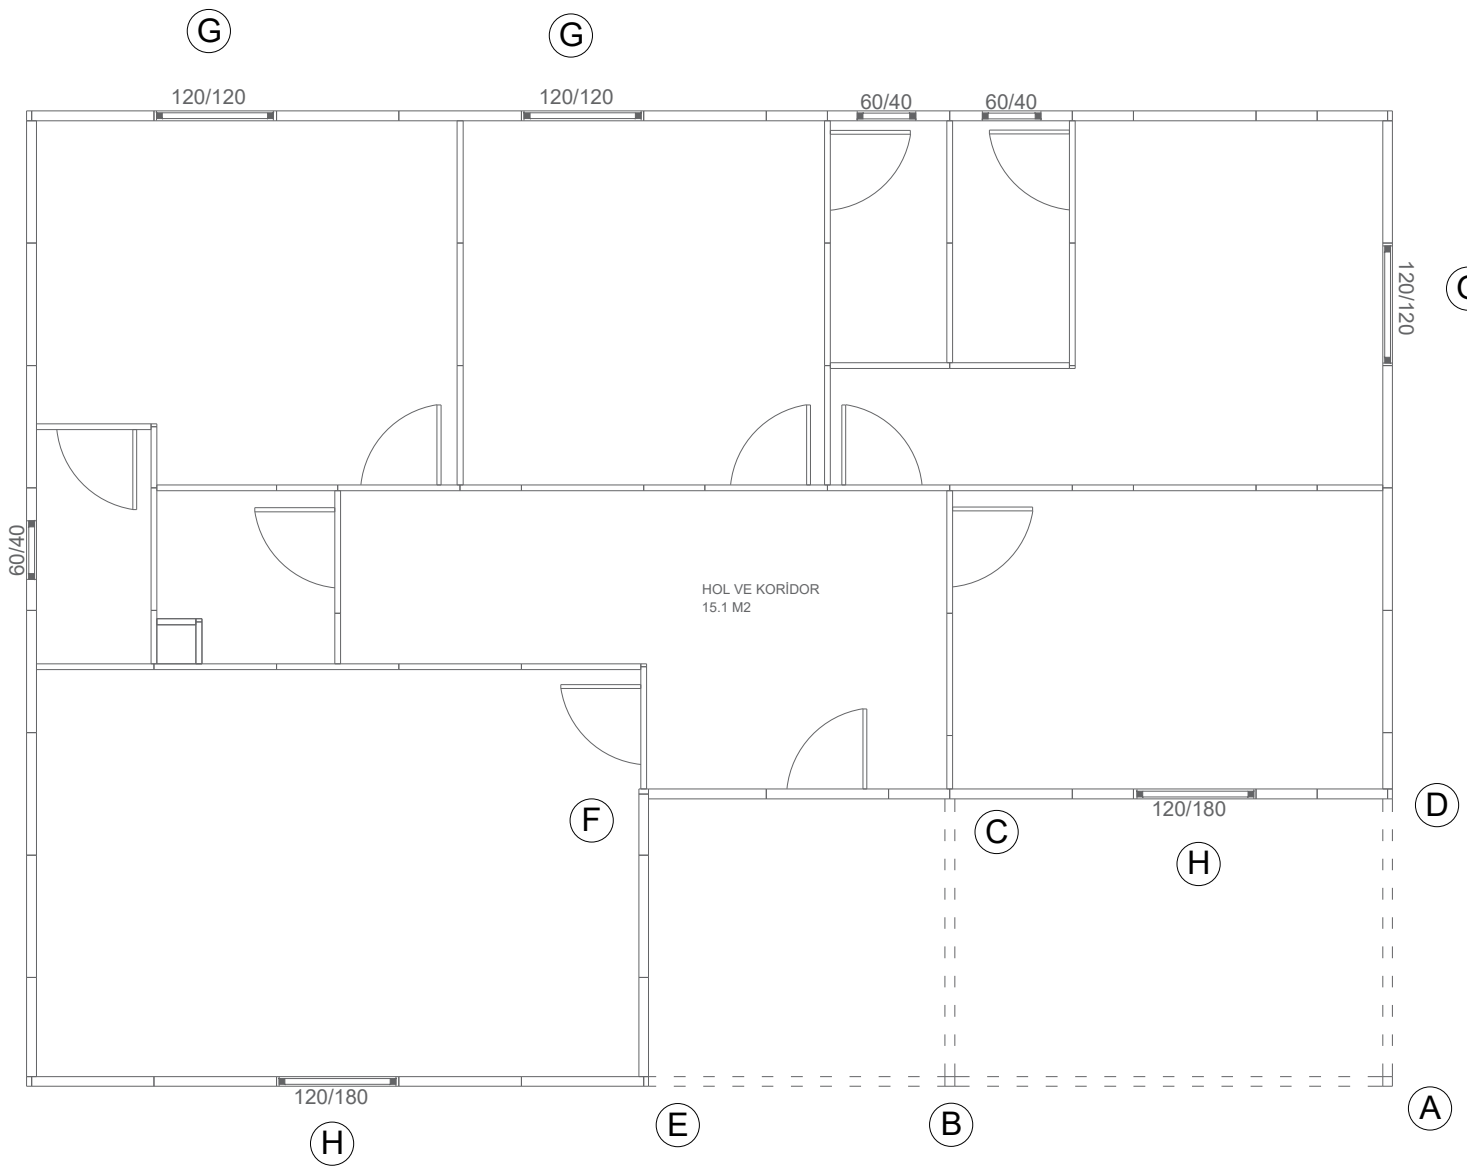

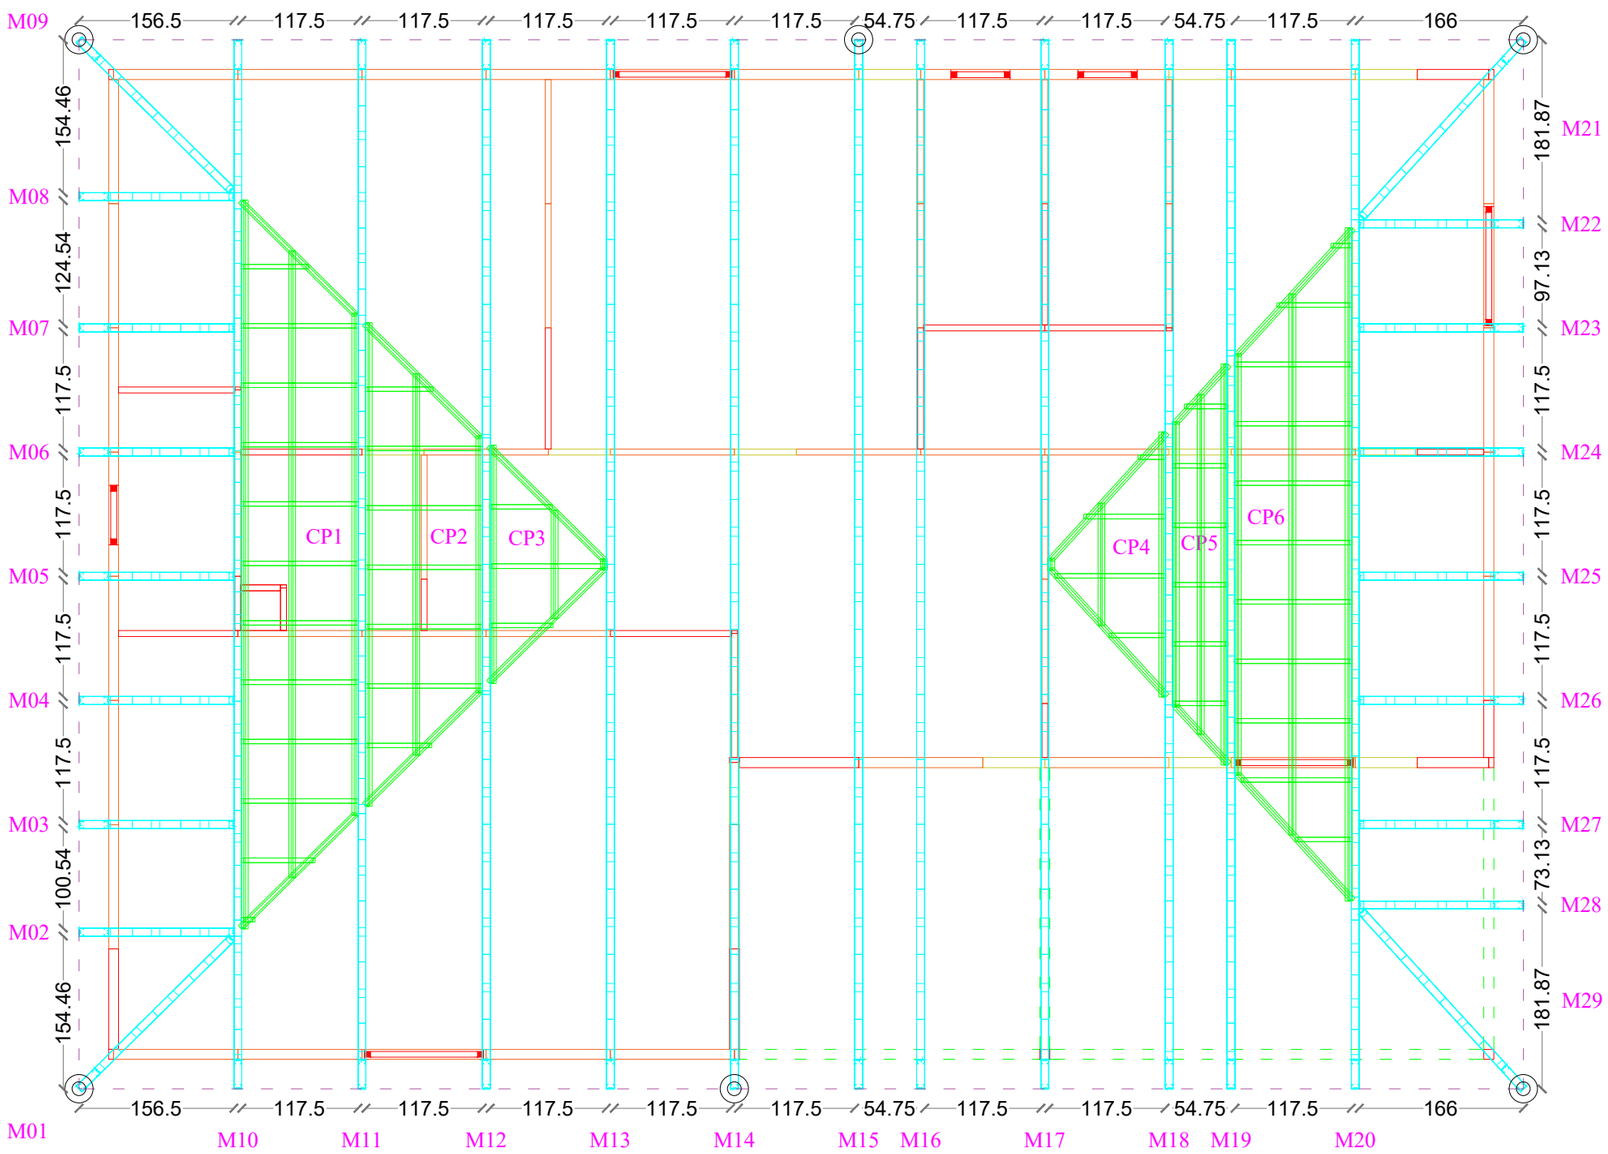

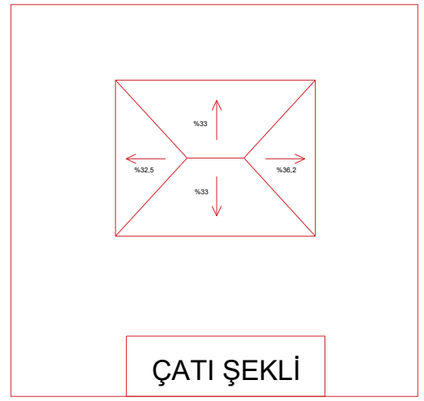

MAKAS VE DERE YERLEŞİM PLANI

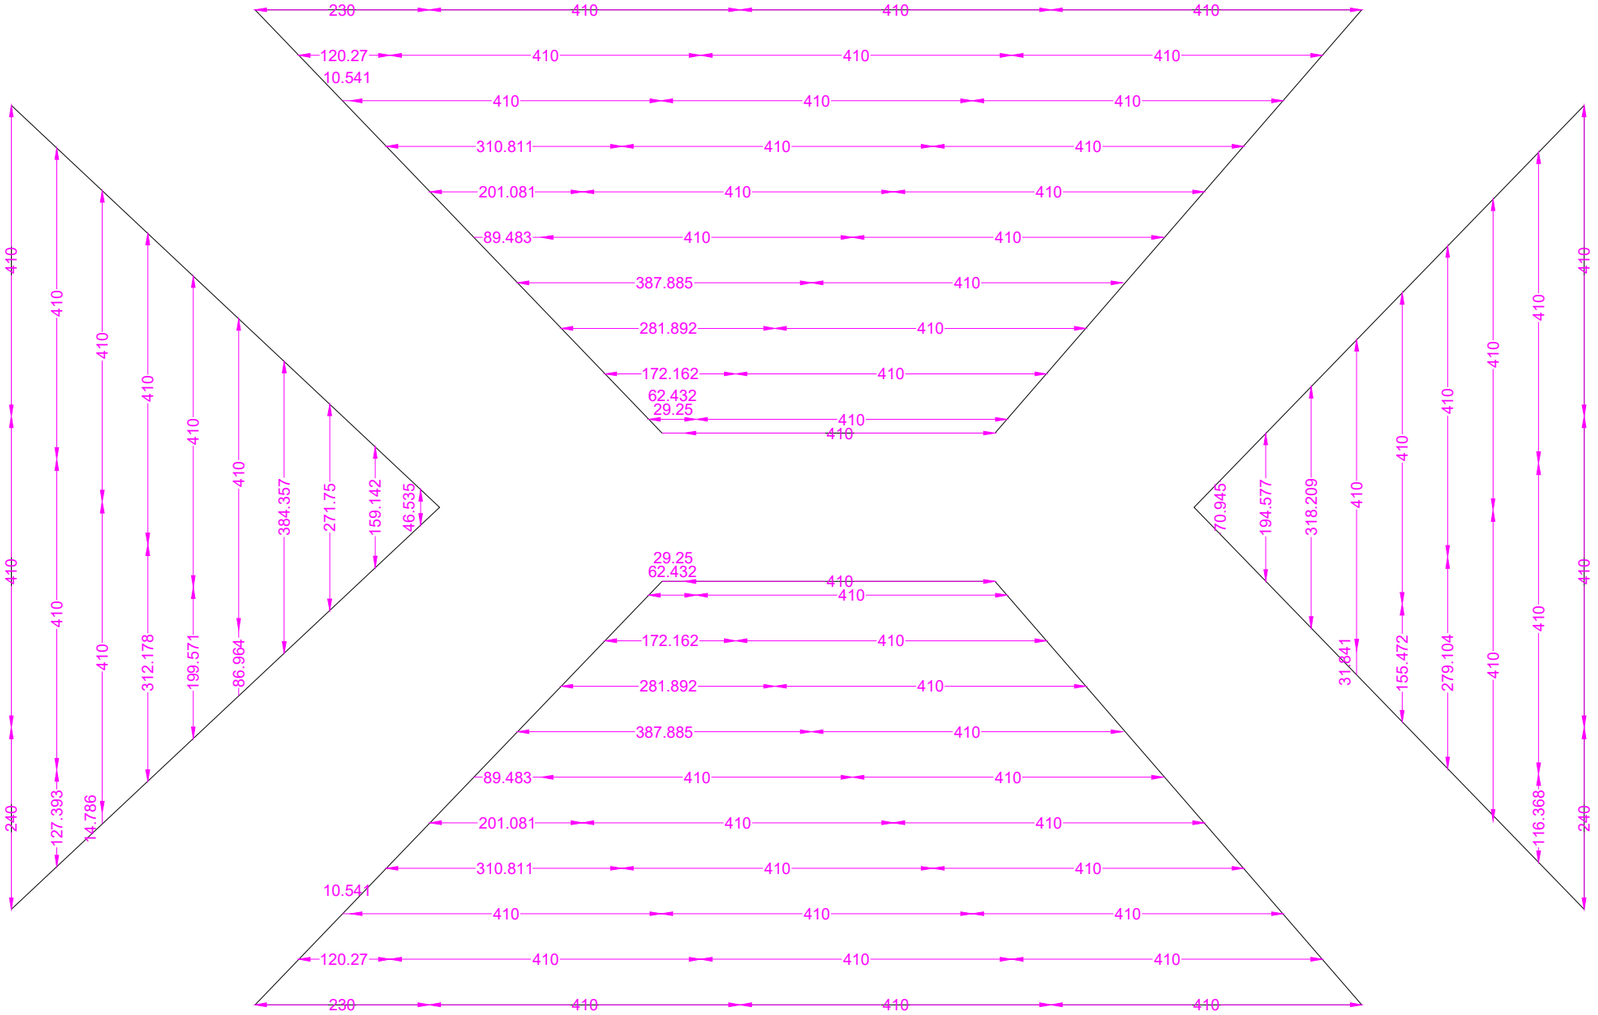


AŞIK YERLEŞİM PLANI


1-) Aşıklar 60 cm aralıklarla monte edilecektir

2-) Mahya aşığı 20 cm de monte edilecektir


MONTAJ DETAYLARI

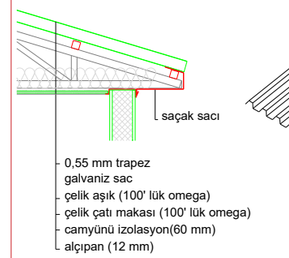



Çatı Detayı

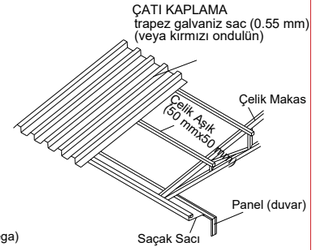


Çatı Detayı

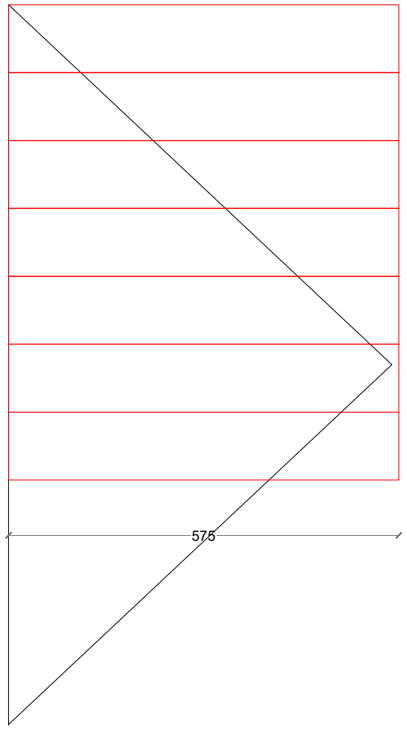

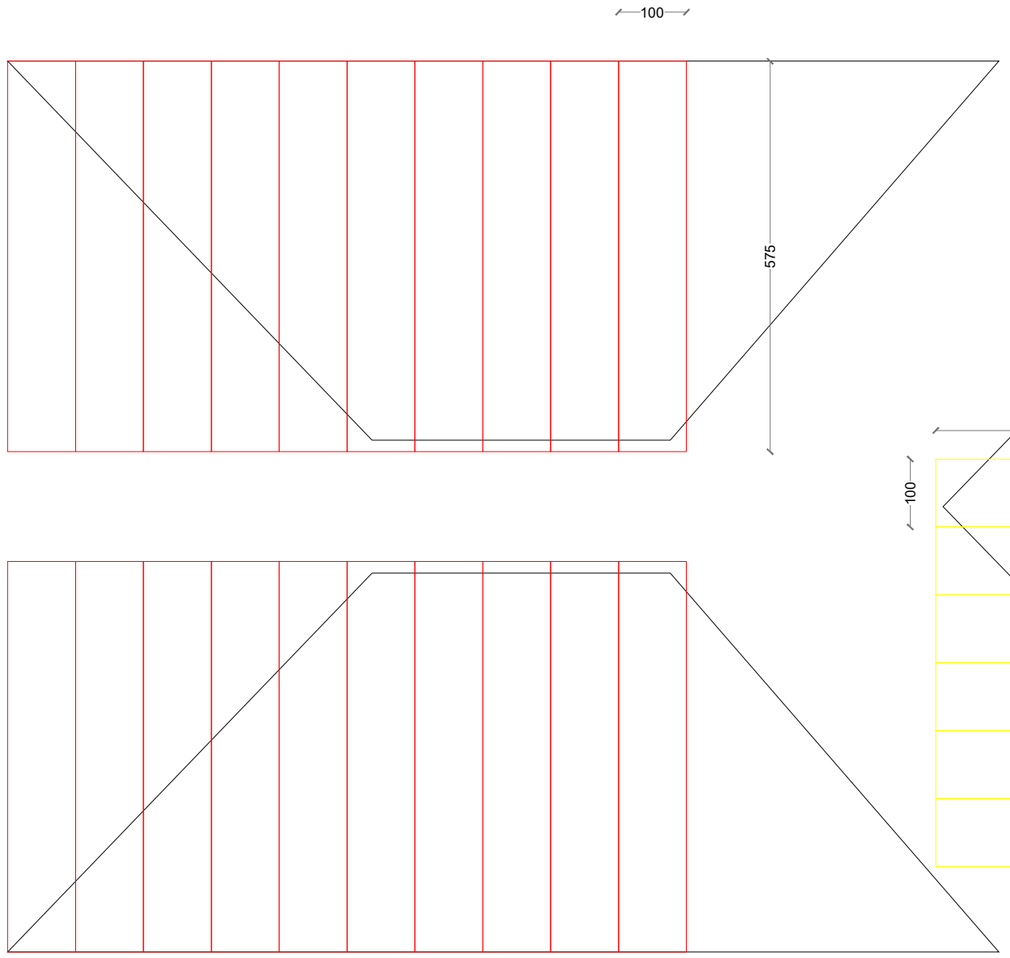

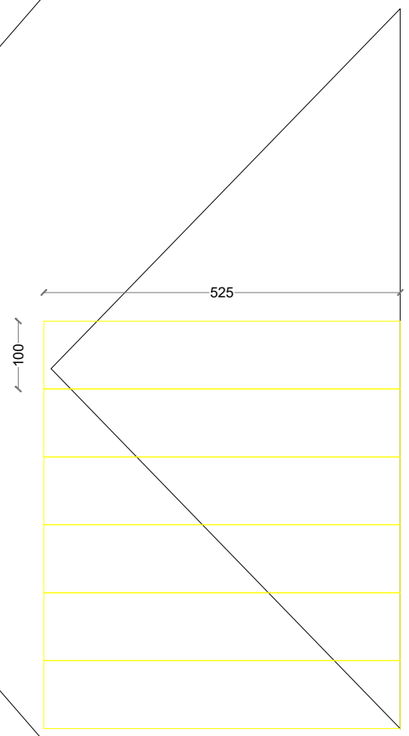

MODERN PREFABRIK 140 M2
ÇATI KAPLAMA MALZEMESİ

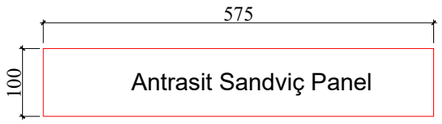


27 Adet

6 Adet

Çatı Alanı:163 m2
Kaplama Alanı:186 m2

ÇATI KAPLAMASI YERLEŞİM PLANI
(KAPLAMA MALZEMESİ)

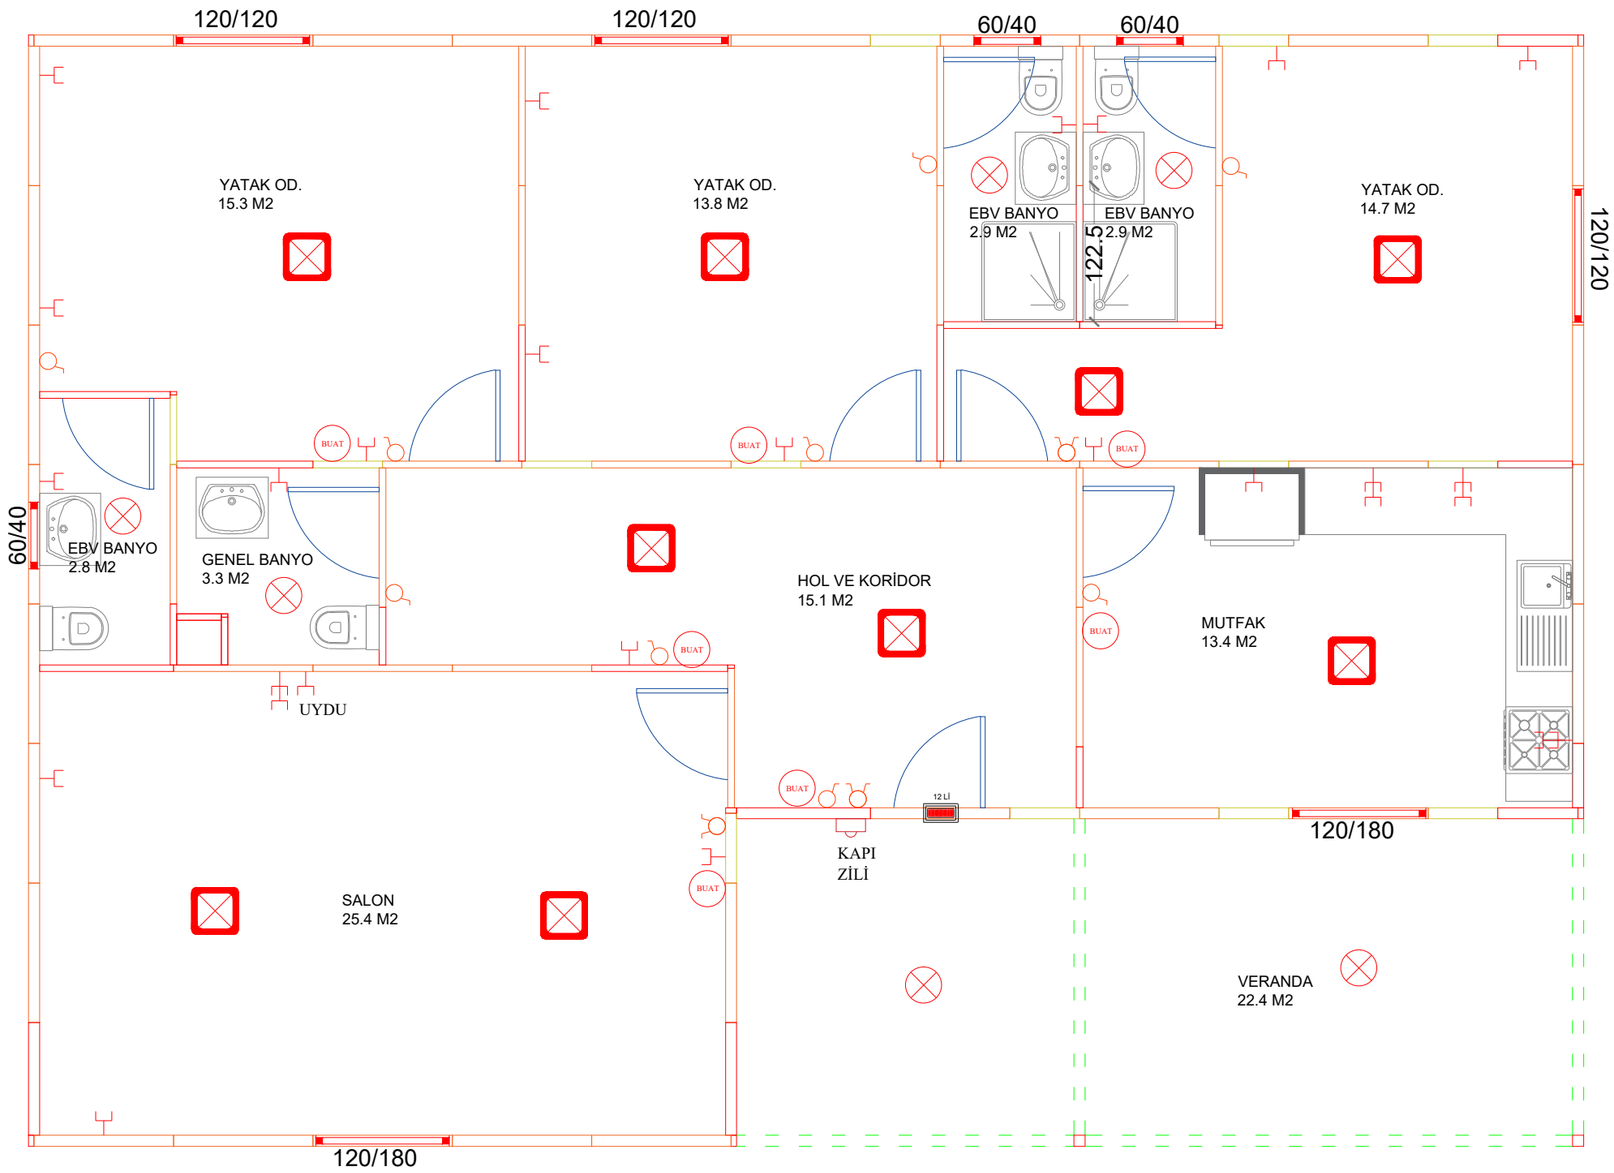

ELEKTRİK PLANI